

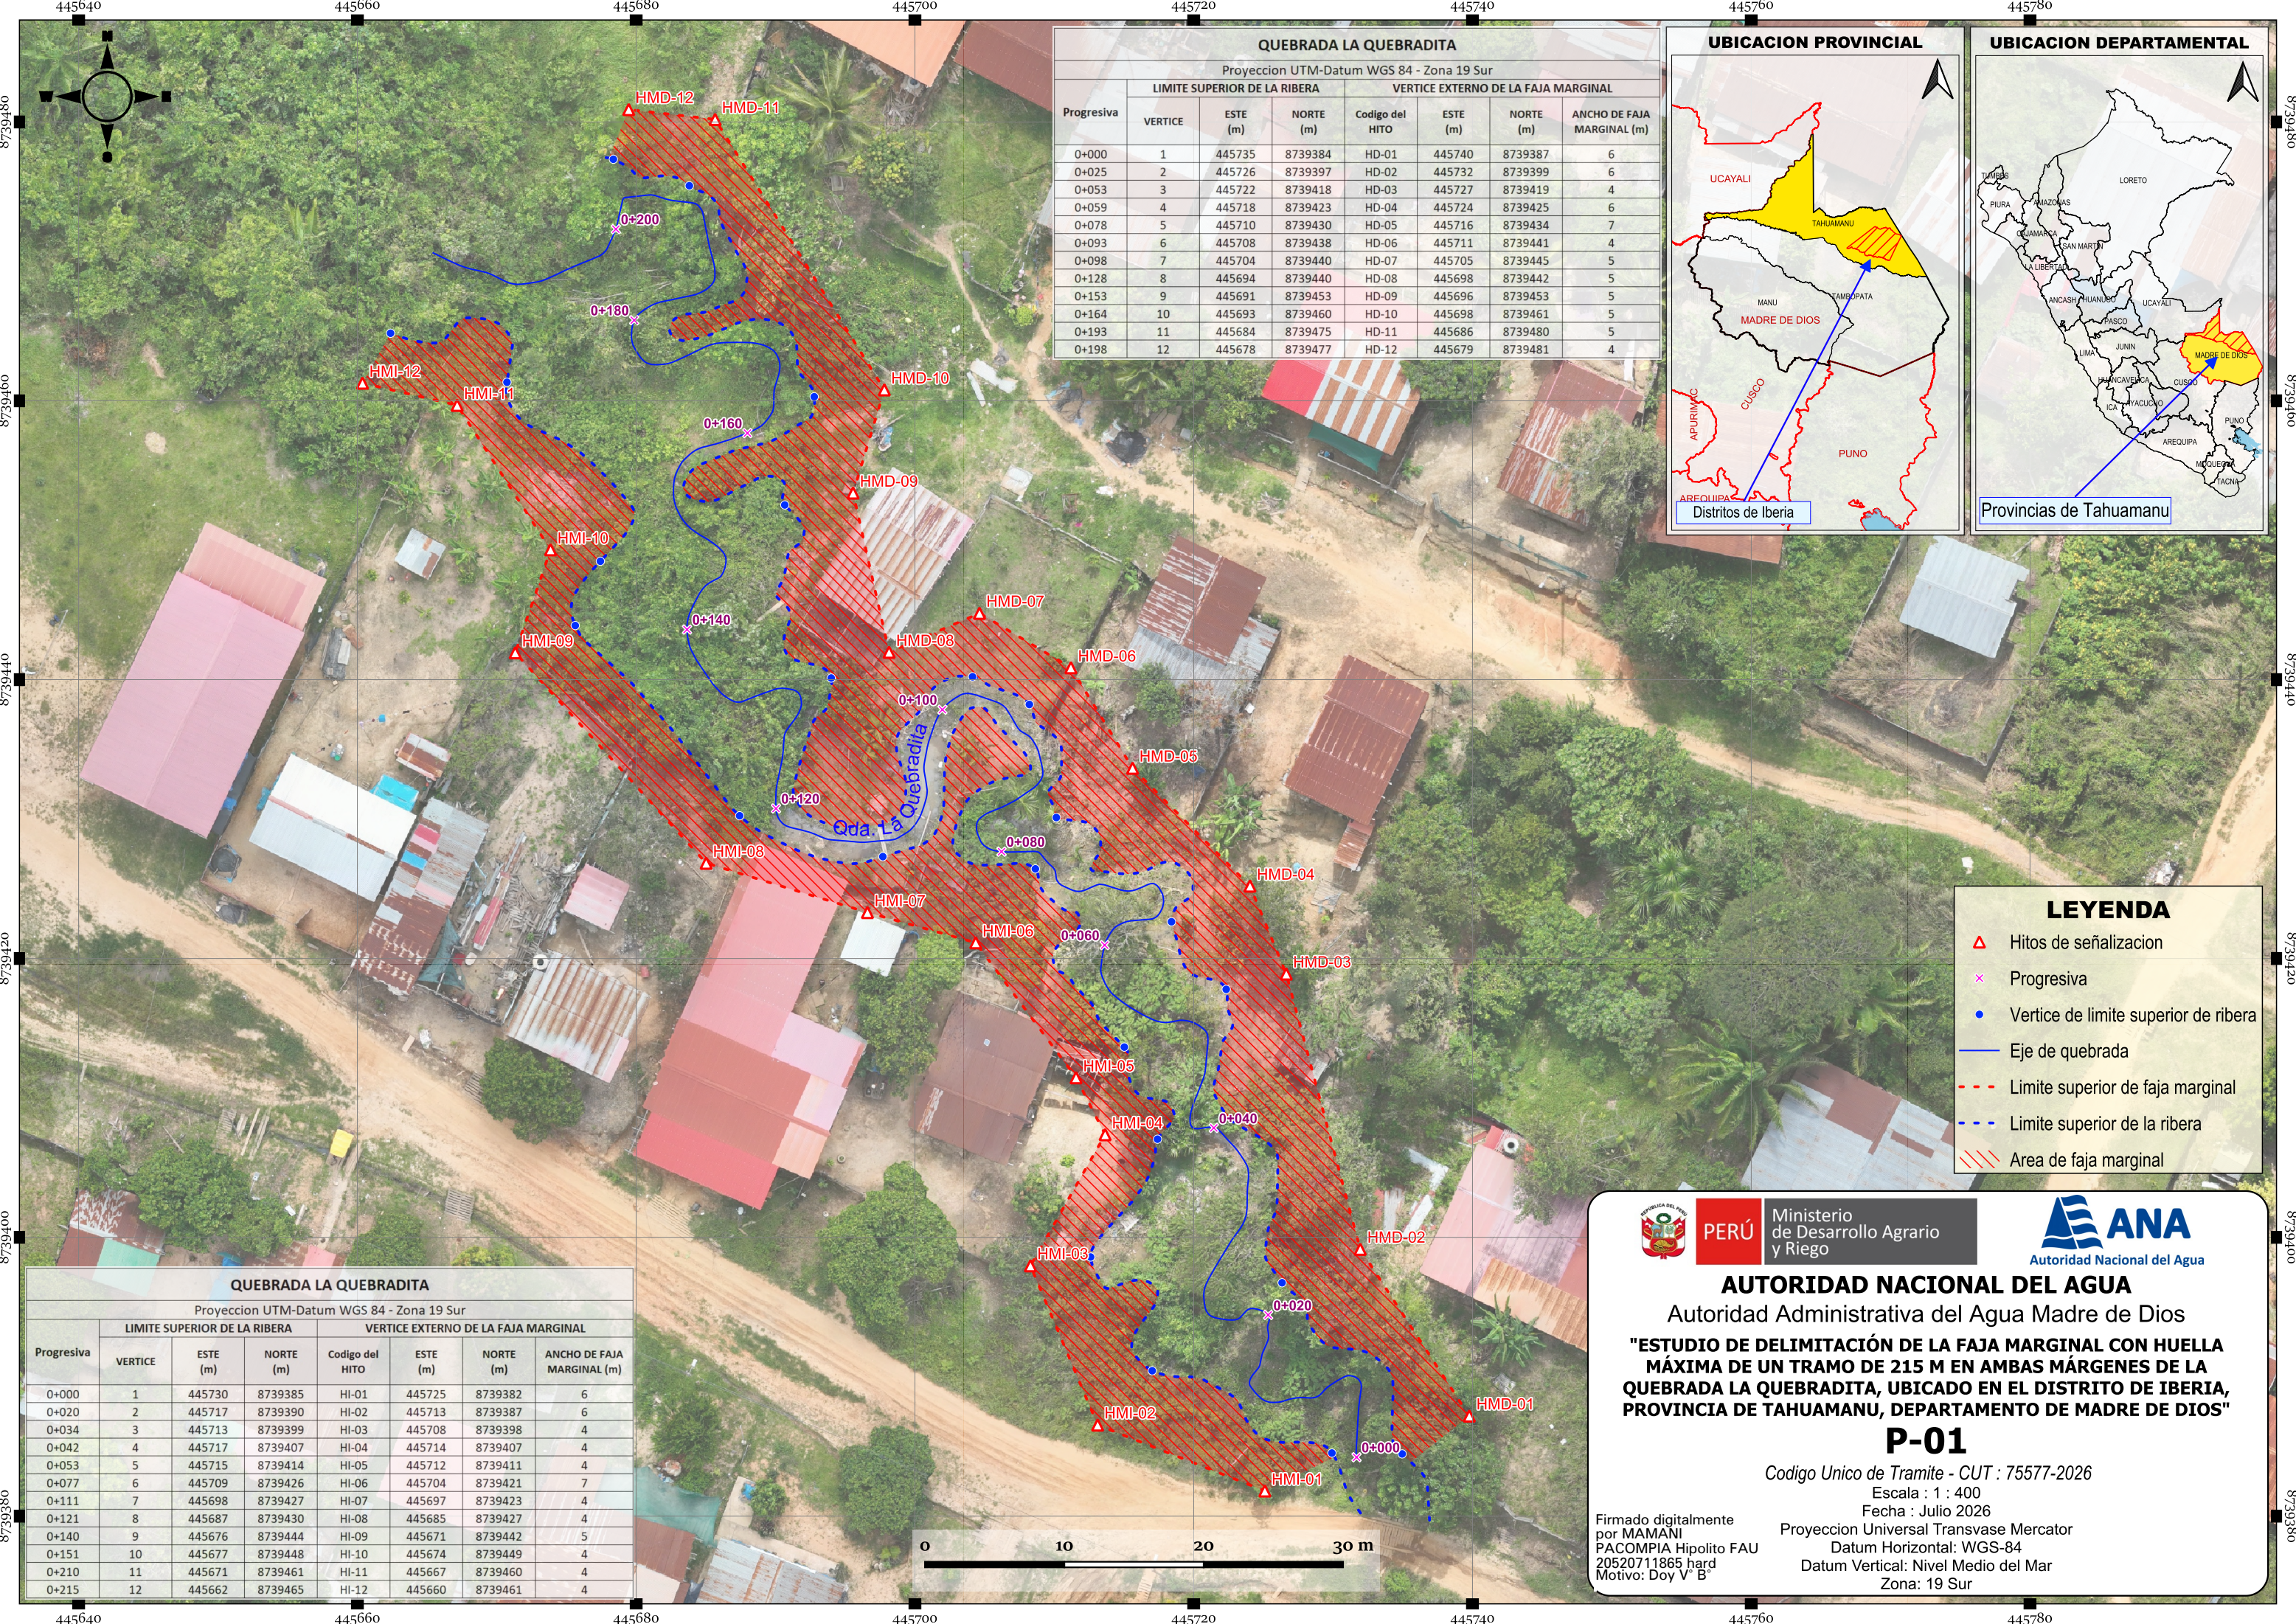


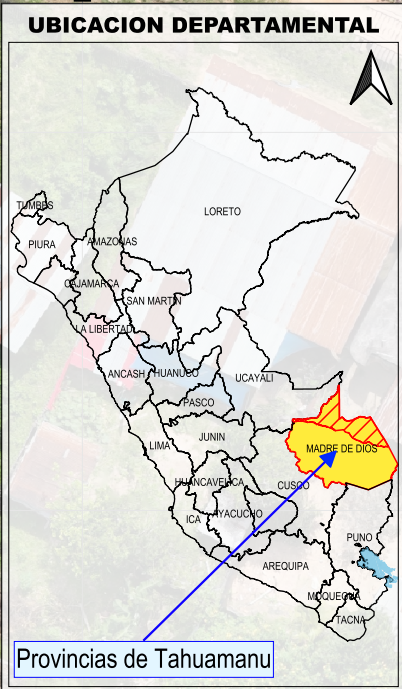

QUEBRADA LA QUEBRADITA							
Proyeccion UTM-Datum WGS 84 - Zona 19 Sur							
Progresiva	LIMITE SUPERIOR DE LA RIBERA			VERTICE EXTERNO DE LA FAJA MARGINAL			
	VERTICE	ESTE (m)	NORTE (m)	Codigo del HITO	ESTE (m)	NORTE (m)	ANCHO DE FAJA MARGINAL (m)
0+000	1	445735	8739384	HD-01	445740	8739387	6
0+025	2	445726	8739397	HD-02	445732	8739399	6
0+053	3	445722	8739418	HD-03	445727	8739419	4
0+059	4	445718	8739423	HD-04	445724	8739425	6
0+078	5	445710	8739430	HD-05	445716	8739434	7
0+093	6	445708	8739438	HD-06	445711	8739441	4
0+098	7	445704	8739440	HD-07	445705	8739445	5
0+128	8	445694	8739440	HD-08	445698	8739442	5
0+153	9	445691	8739453	HD-09	445696	8739453	5
0+164	10	445693	8739460	HD-10	445698	8739461	5
0+193	11	445684	8739475	HD-11	445686	8739480	5
0+198	12	445678	8739477	HD-12	445679	8739481	4

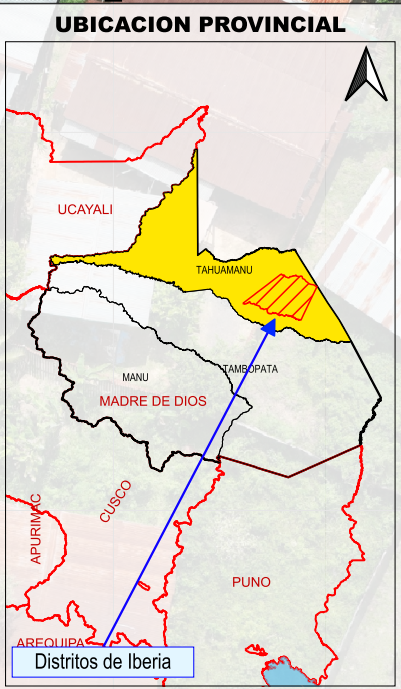

LEYENDA	
	Hitos de señalizacion
	Progresiva
	Vertice de limite superior de ribera
	Eje de quebrada
	Limite superior de faja marginal
	Limite superior de la ribera
	Area de faja marginal

QUEBRADA LA QUEBRADITA

Proyeccion UTM-Datum WGS 84 - Zona 19 Sur

Progresiva	LIMITE SUPERIOR DE LA RIBERA			VERTICE EXTERNO DE LA FAJA MARGINAL			
	VERTICE	ESTE (m)	NORTE (m)	Codigo del HITO	ESTE (m)	NORTE (m)	ANCHO DE FAJA MARGINAL (m)
0+000	1	445730	8739385	HI-01	445725	8739382	6
0+020	2	445717	8739390	HI-02	445713	8739387	6
0+034	3	445713	8739399	HI-03	445708	8739398	4
0+042	4	445717	8739407	HI-04	445714	8739407	4
0+053	5	445715	8739414	HI-05	445712	8739411	4
0+077	6	445709	8739426	HI-06	445704	8739421	7
0+111	7	445698	8739427	HI-07	445697	8739423	4
0+121	8	445687	8739430	HI-08	445685	8739427	4
0+140	9	445676	8739444	HI-09	445671	8739442	5
0+151	10	445677	8739448	HI-10	445674	8739449	4
0+210	11	445671	8739461	HI-11	445667	8739460	4
0+215	12	445662	8739465	HI-12	445660	8739461	4



PERÚ

Ministerio de Desarrollo Agrario y Riego



AUTORIDAD NACIONAL DEL AGUA

Autoridad Administrativa del Agua Madre de Dios

"ESTUDIO DE DELIMITACIÓN DE LA FAJA MARGINAL CON HUELLA MÁXIMA DE UN TRAMO DE 215 M EN AMBAS MÁRGENES DE LA QUEBRADA LA QUEBRADITA, UBICADO EN EL DISTRITO DE IBERIA, PROVINCIA DE TAHUAMANU, DEPARTAMENTO DE MADRE DE DIOS"

P-01

Codigo Unico de Tramite - CUT : 75577-2026

Escala : 1 : 400

Fecha : Julio 2026

Proyeccion Universal Transvase Mercator

Datum Horizontal: WGS-84

Datum Vertical: Nivel Medio del Mar

Zona: 19 Sur

Firmado digitalmente por MAMANI PACOMPIA Hipolito FAU 20520711865 hard Motivo: Doy V° B°