
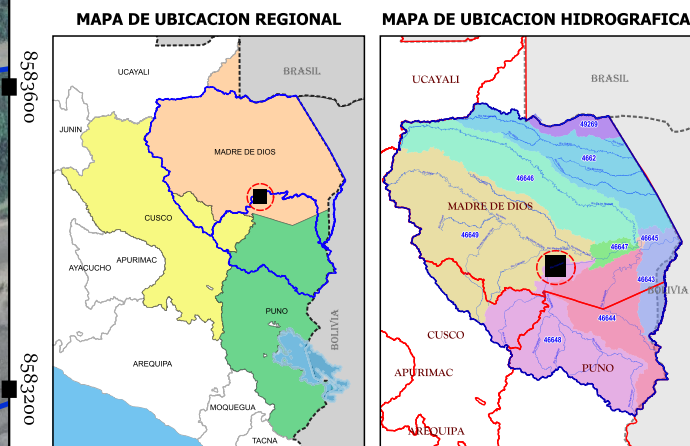
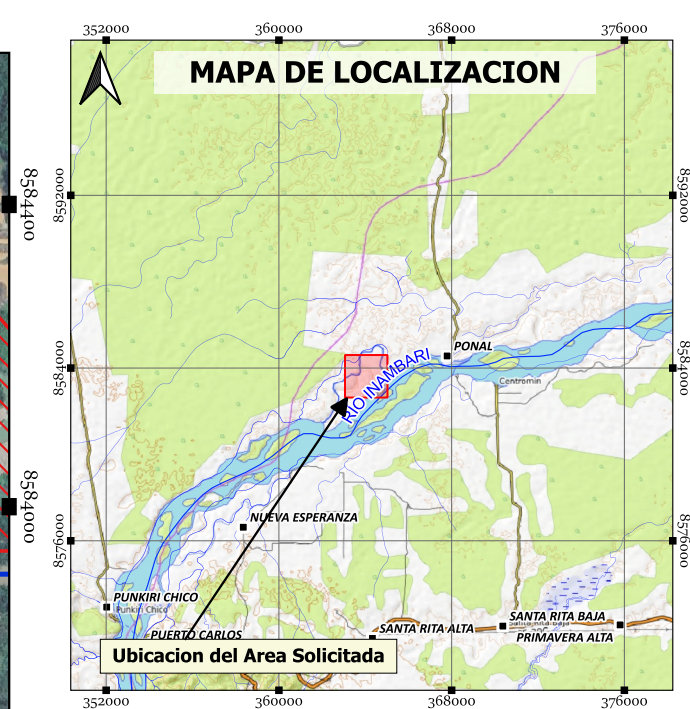


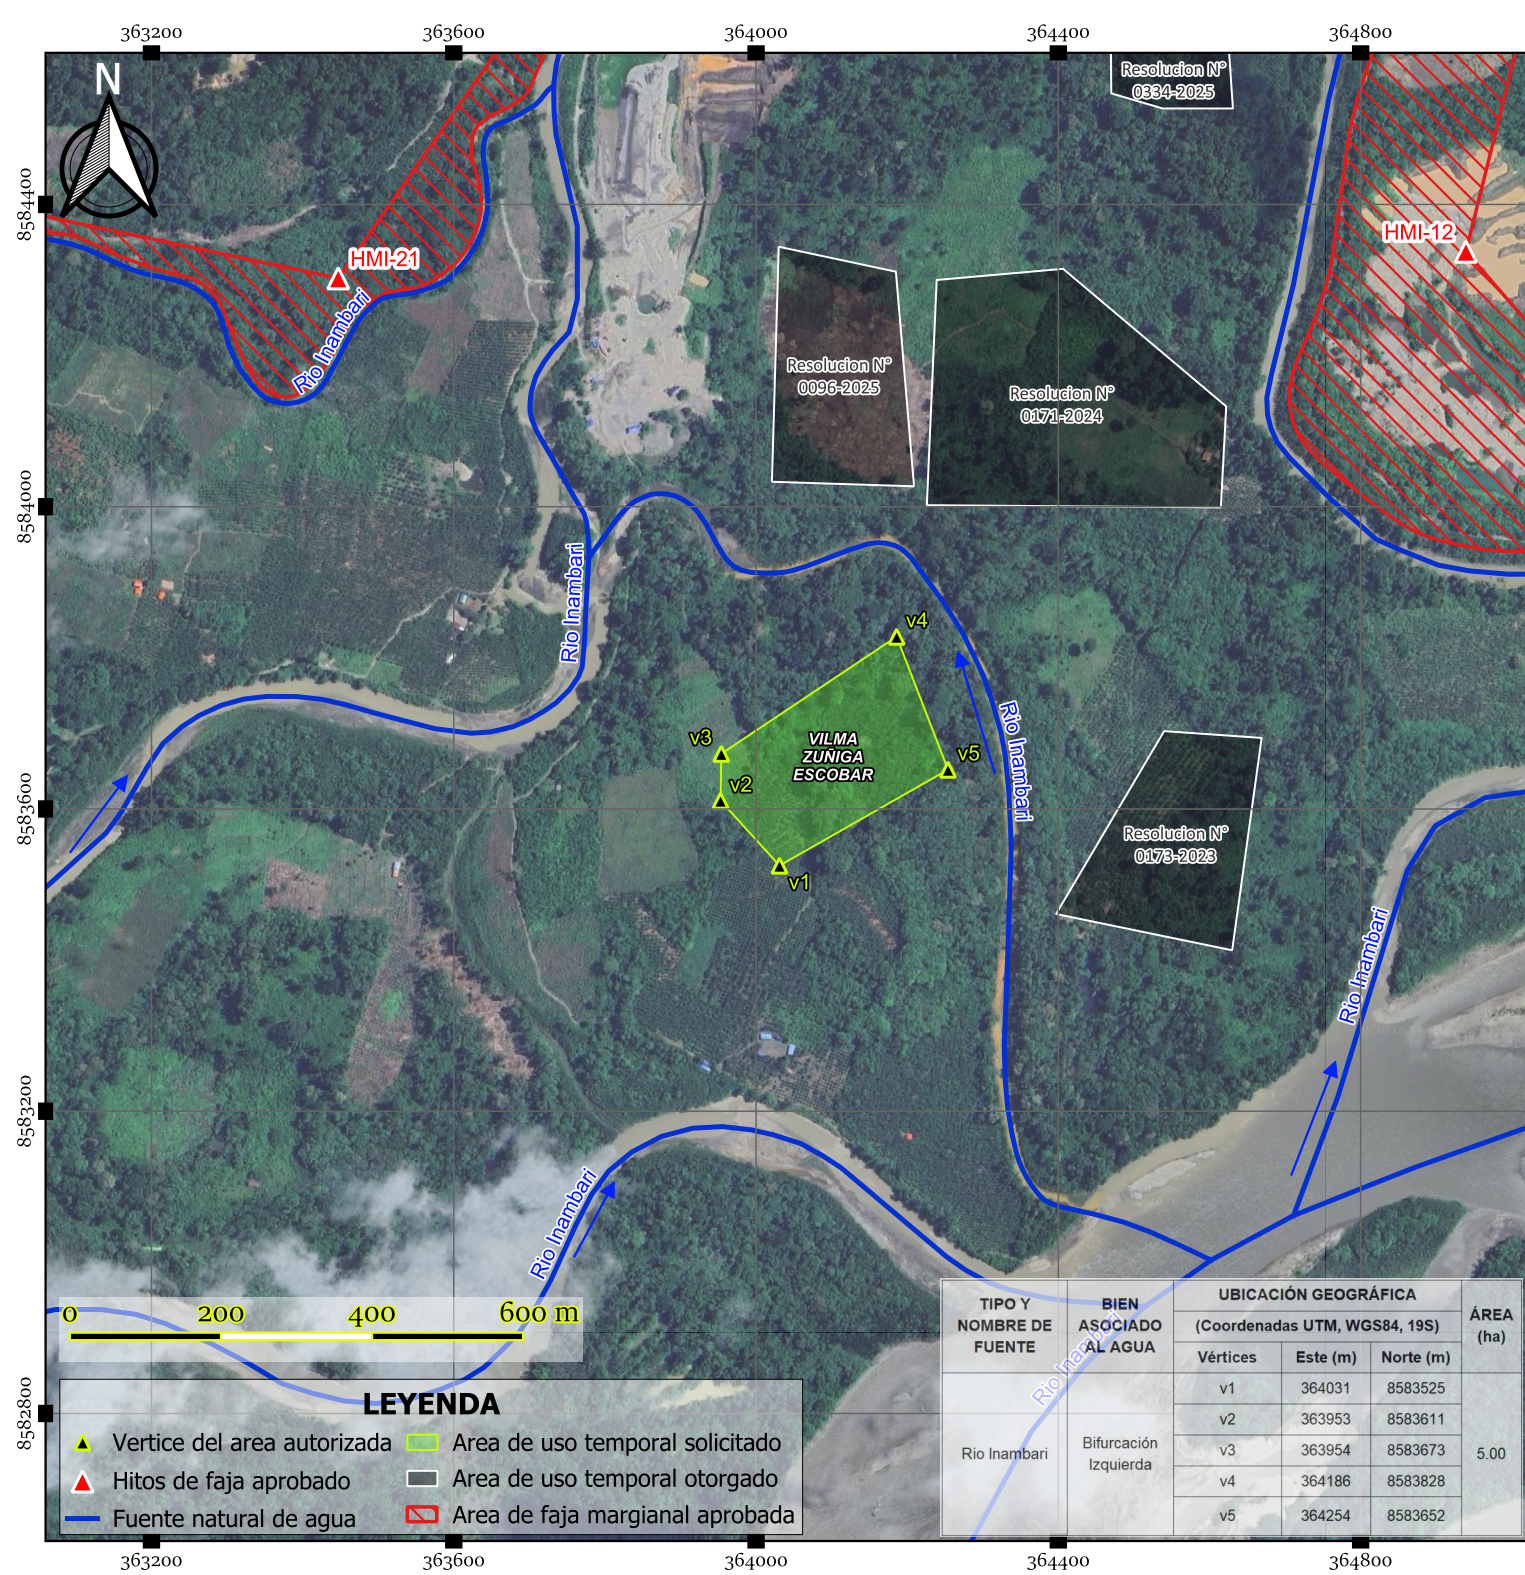

PERÚ Ministerio de Desarrollo Agrario y Riego

ANA Autoridad Nacional del Agua

Titular: VILMA ZUÑIGA ESCOBAR, con DNI N° 10449912

Proyecto: AUTORIZACIÓN DE USO TEMPORAL DE TERRENO DE LA BIFURCACIÓN IZQUIERDA DEL RÍO INAMBARÍ, PARA SIEMBRA DE CULTIVOS

Procedimiento: AUTORIZACIÓN PARA EL USO TEMPORAL DE LAS FAJAS MARGINALES Y DE LAS RIBERAS DE LOS RÍOS AMAZONICOS PARA LA SIEMBRA DE CULTIVOS

Código Único de Trámite - CUT : 47056-2026
Escala : 1 : 10 000
Fecha : Mayo 2026
Proyección Universal Transverse Mercator
Datum Horizontal : WGS 84
Datum Vertical : Nivel Medio del Mar
Zona : 19 Sur