
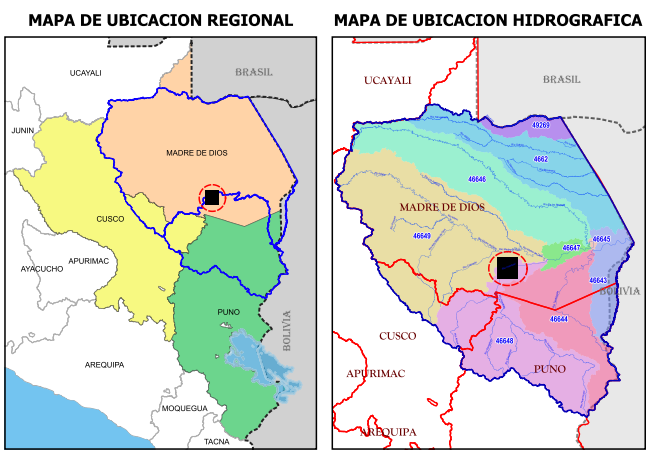


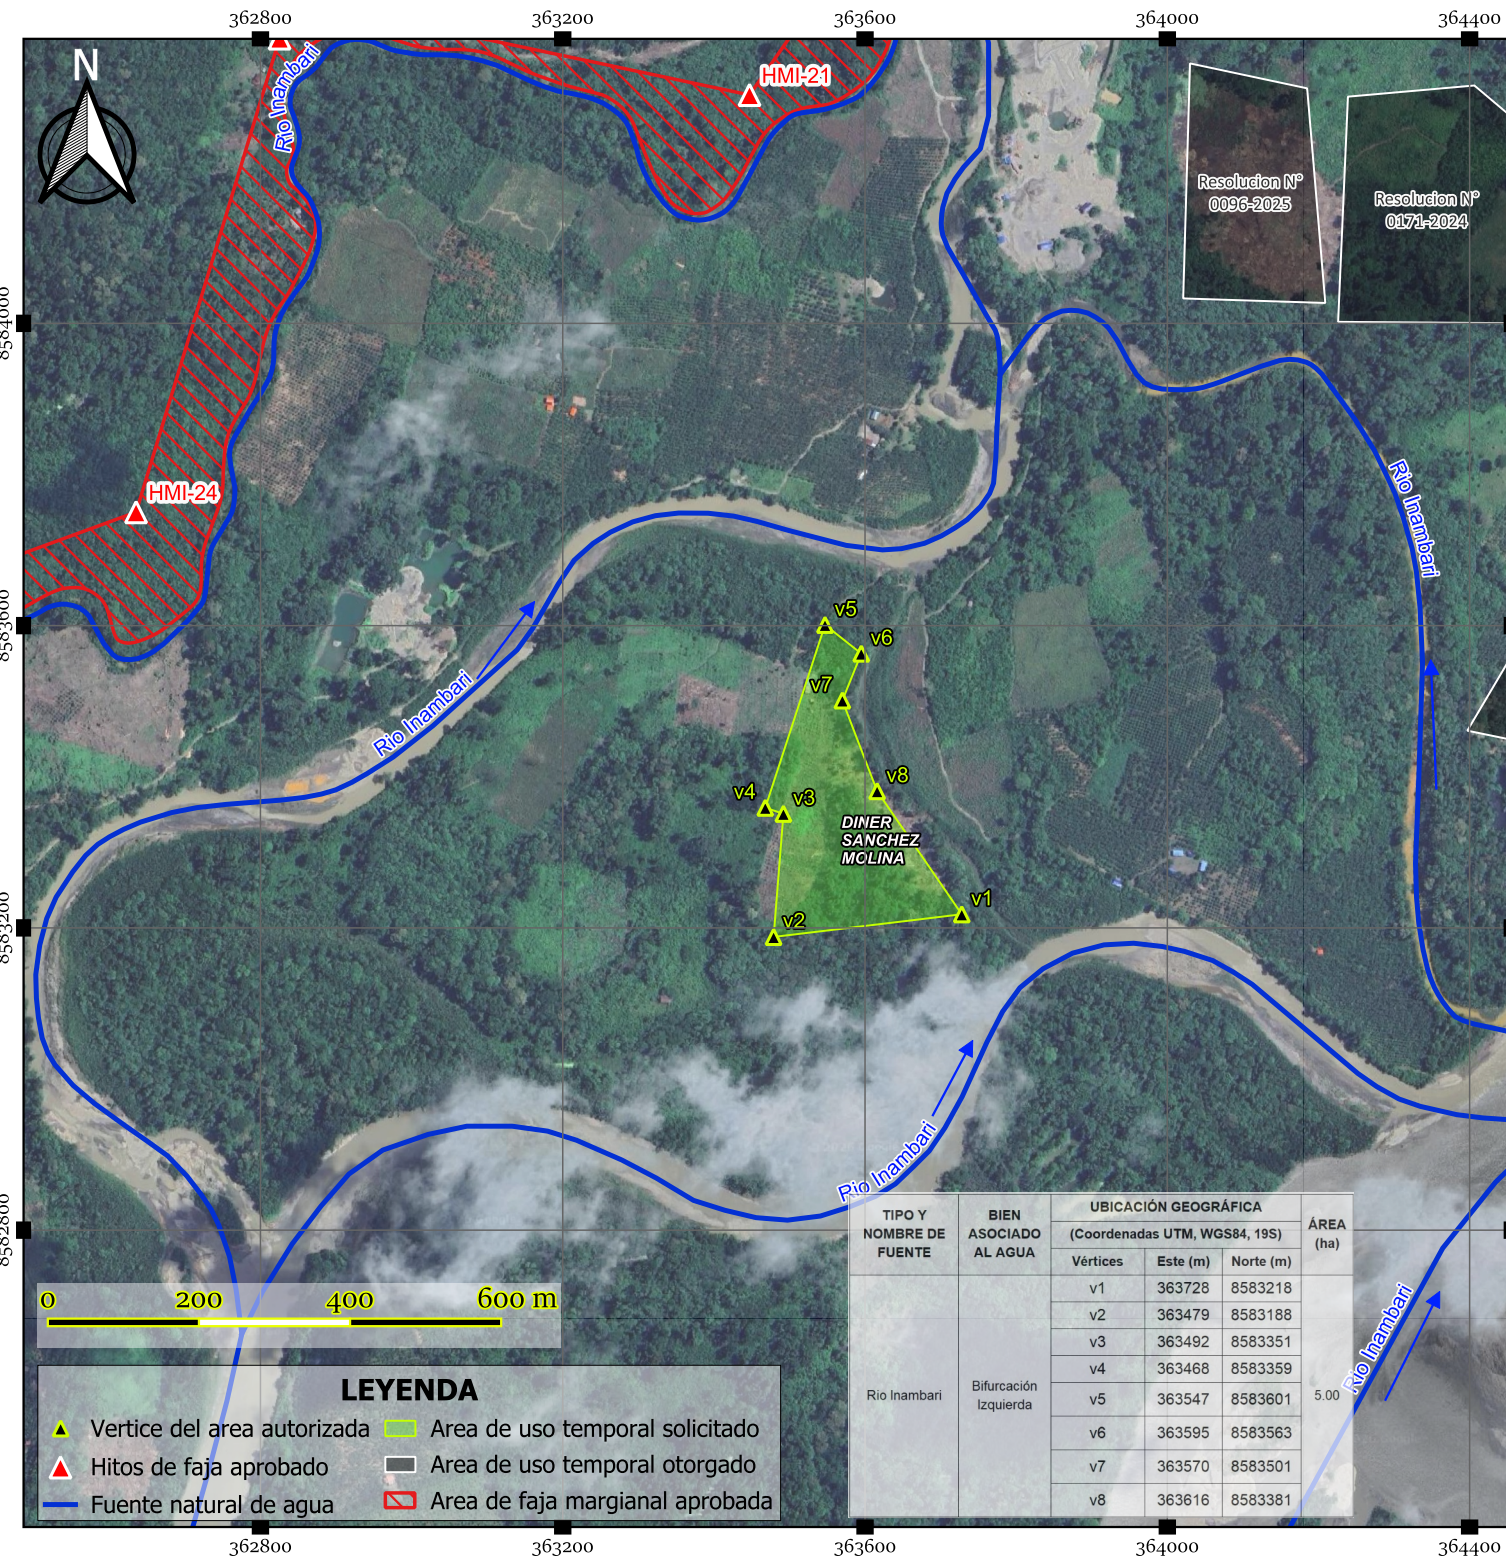

Ministerio de Desarrollo Agrario y Riego
ANA
Autoridad Nacional del Agua

Titular : DINER SANCHEZ MOLINA, con DNI N° 71515428

Proyecto : AUTORIZACIÓN DE USO TEMPORAL DE TERRENO DE LA BIFURCACION IZQUIERDA DEL RÍO INAMBARÍ, PARA SIEMBRA DE CULTIVOS

Procedimiento : AUTORIZACION PARA EL USO TEMPORAL DE LAS FAJAS MARGINALES Y DE LAS RIBERAS DE LOS RIOS AMAZONICOS PARA LA SIEMBRA DE CULTIVOS

Codigo Unico de Tramite - CUT : 67767-2026
Escala : 1 : 10 000
Fecha : Mayo 2026

Firmado digitalmente por MAMANI FACOMPIA Hipolito
FAU 20520711865 hard
Motivo: Doy V° B°

Proyeccion Universal Transverse Mercator
Datum Horizontal : WGS 84
Datum Vertical : Nivel Medio del Mar
Zona : 19 Sur

TIPO Y NOMBRE DE FUENTE	BIEN ASOCIADO AL AGUA	UBICACIÓN GEOGRÁFICA (Coordenadas UTM, WGS84, 19S)			ÁREA (ha)
		Vértices	Este (m)	Norte (m)	
Rio Inambari	Bifurcación Izquierda	v1	363728	8583218	5.00
		v2	363479	8583188	
		v3	363492	8583351	
		v4	363468	8583359	
		v5	363547	8583601	
		v6	363595	8583563	
		v7	363570	8583501	
		v8	363616	8583381	