
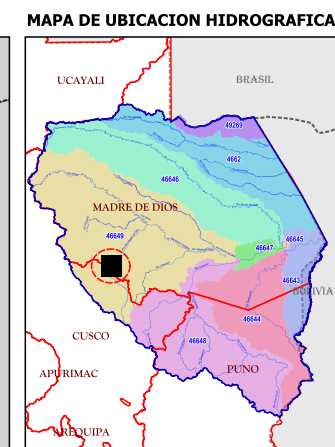
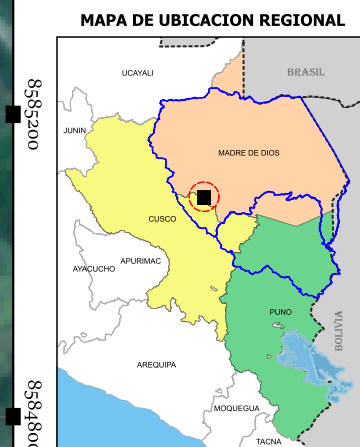


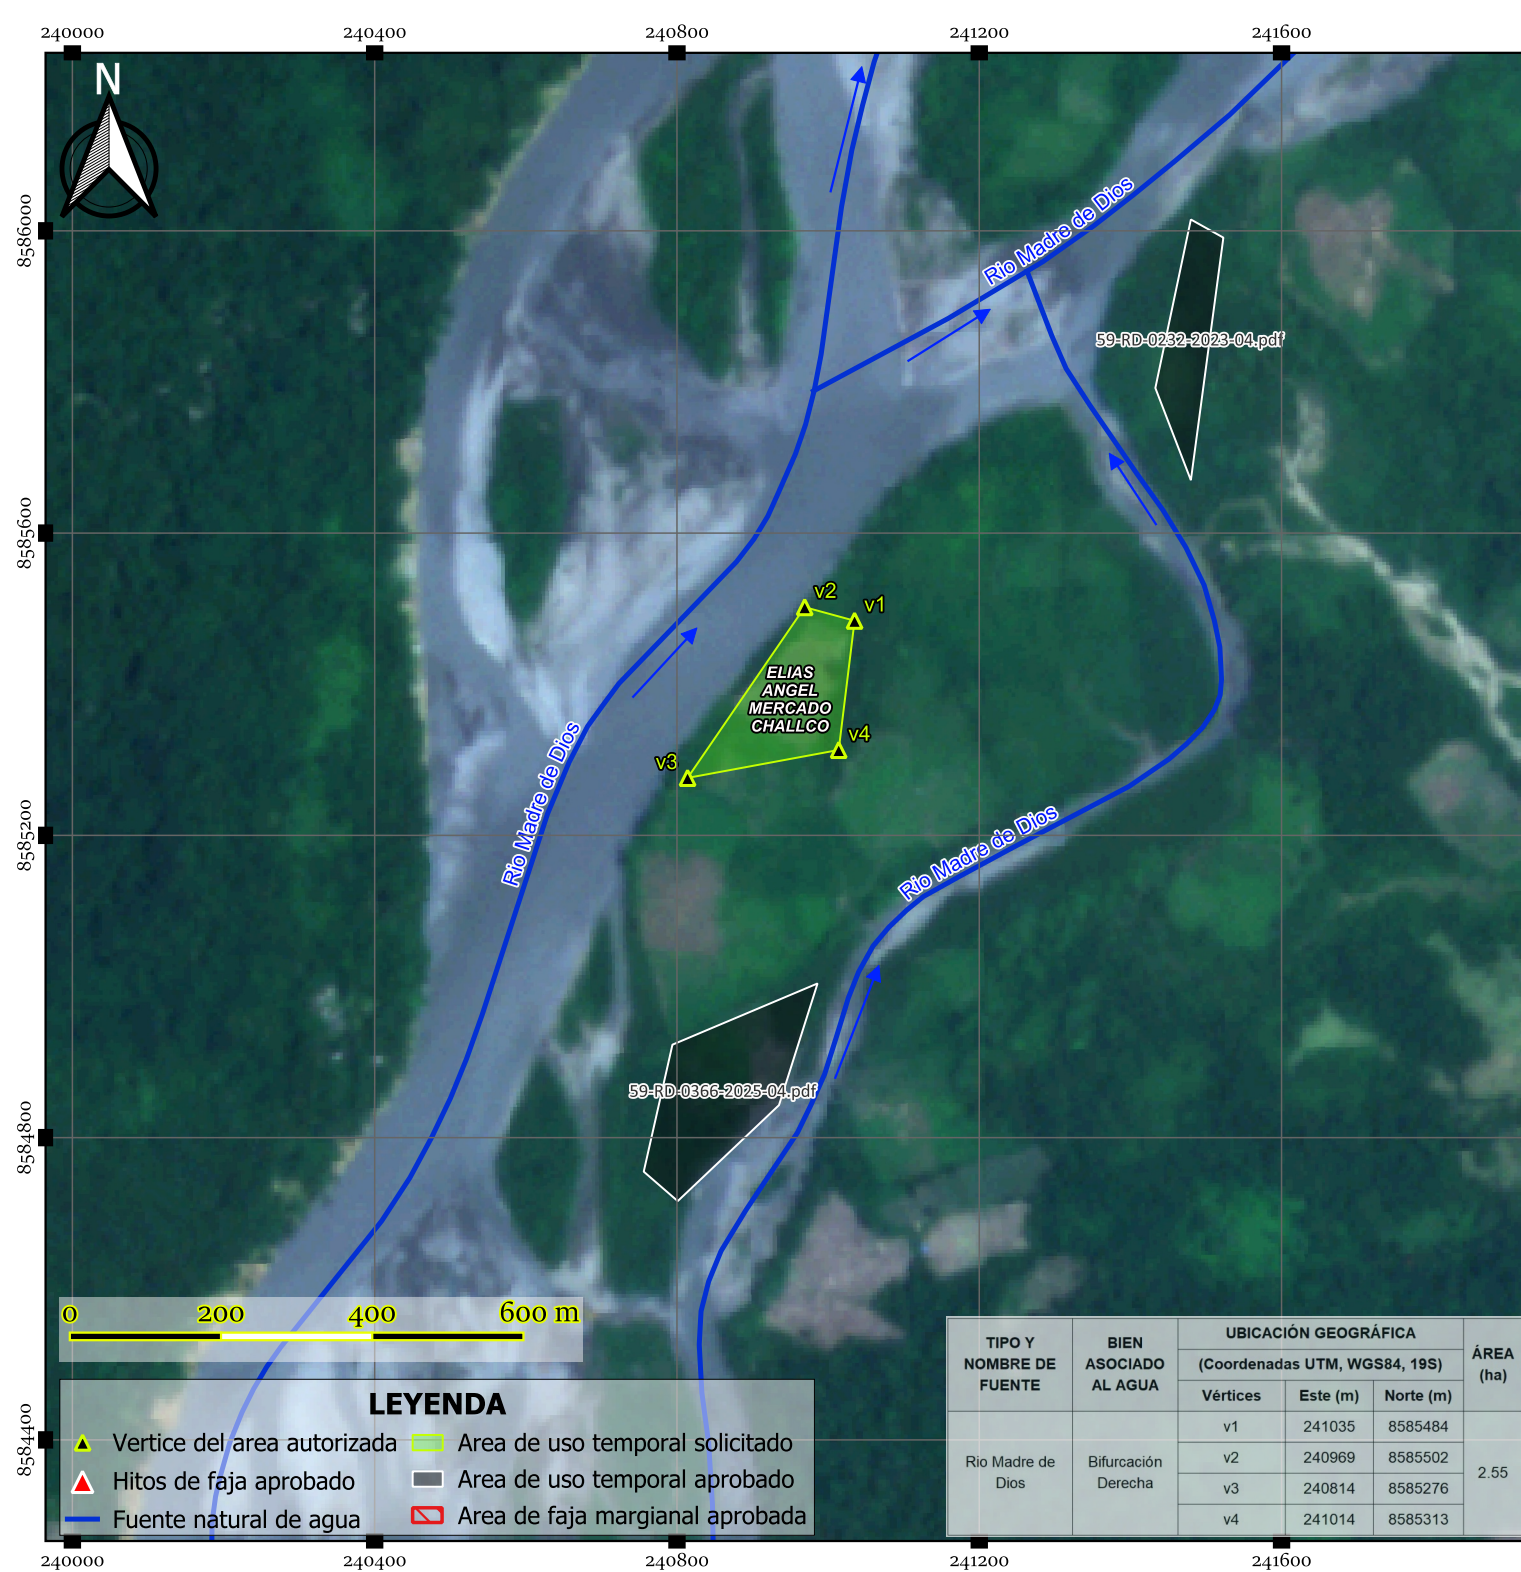

PERÚ Ministerio de Desarrollo Agrario y Riego

ANA Autoridad Nacional del Agua

Titular: ELIAS ANGEL MERCADO CHALLCO, con DNI N° 42111809

Proyecto: AUTORIZACIÓN DE USO TEMPORAL DE TERRENO DE LA BIFURCACIÓN DERECHA DEL RÍO MADRE DE DIOS, PARA SIEMBRA DE CULTIVOS

Procedimiento: AUTORIZACIÓN PARA EL USO TEMPORAL DE LAS FAJAS MARGINALES Y DE LAS RIBERAS DE LOS RÍOS AMAZONICOS PARA LA SIEMBRA DE CULTIVOS

Código Único de Trámite - CUT : 95688-2026

Escala : 1 : 10 000

Fecha : Julio 2026

Firmado digitalmente por MAMANI PACOMPIA Hipólito FAU 20520711865 hard Motivo: Doy V° B°

Proyección Universal Transverse Mercator

Datum Horizontal : WGS 84

Datum Vertical : Nivel Medio del Mar

Zona : 19 Sur