
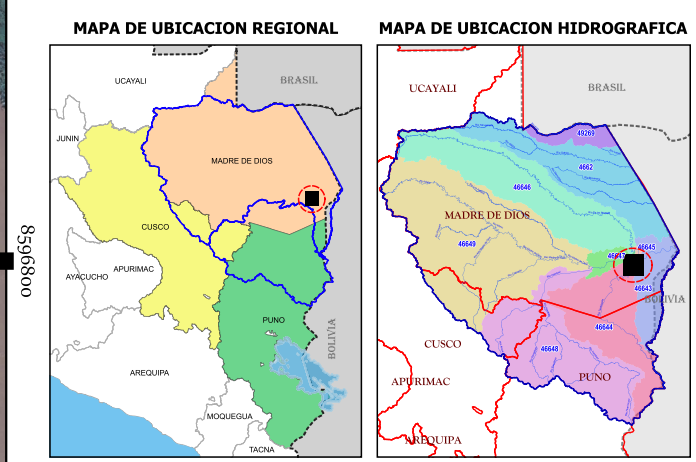


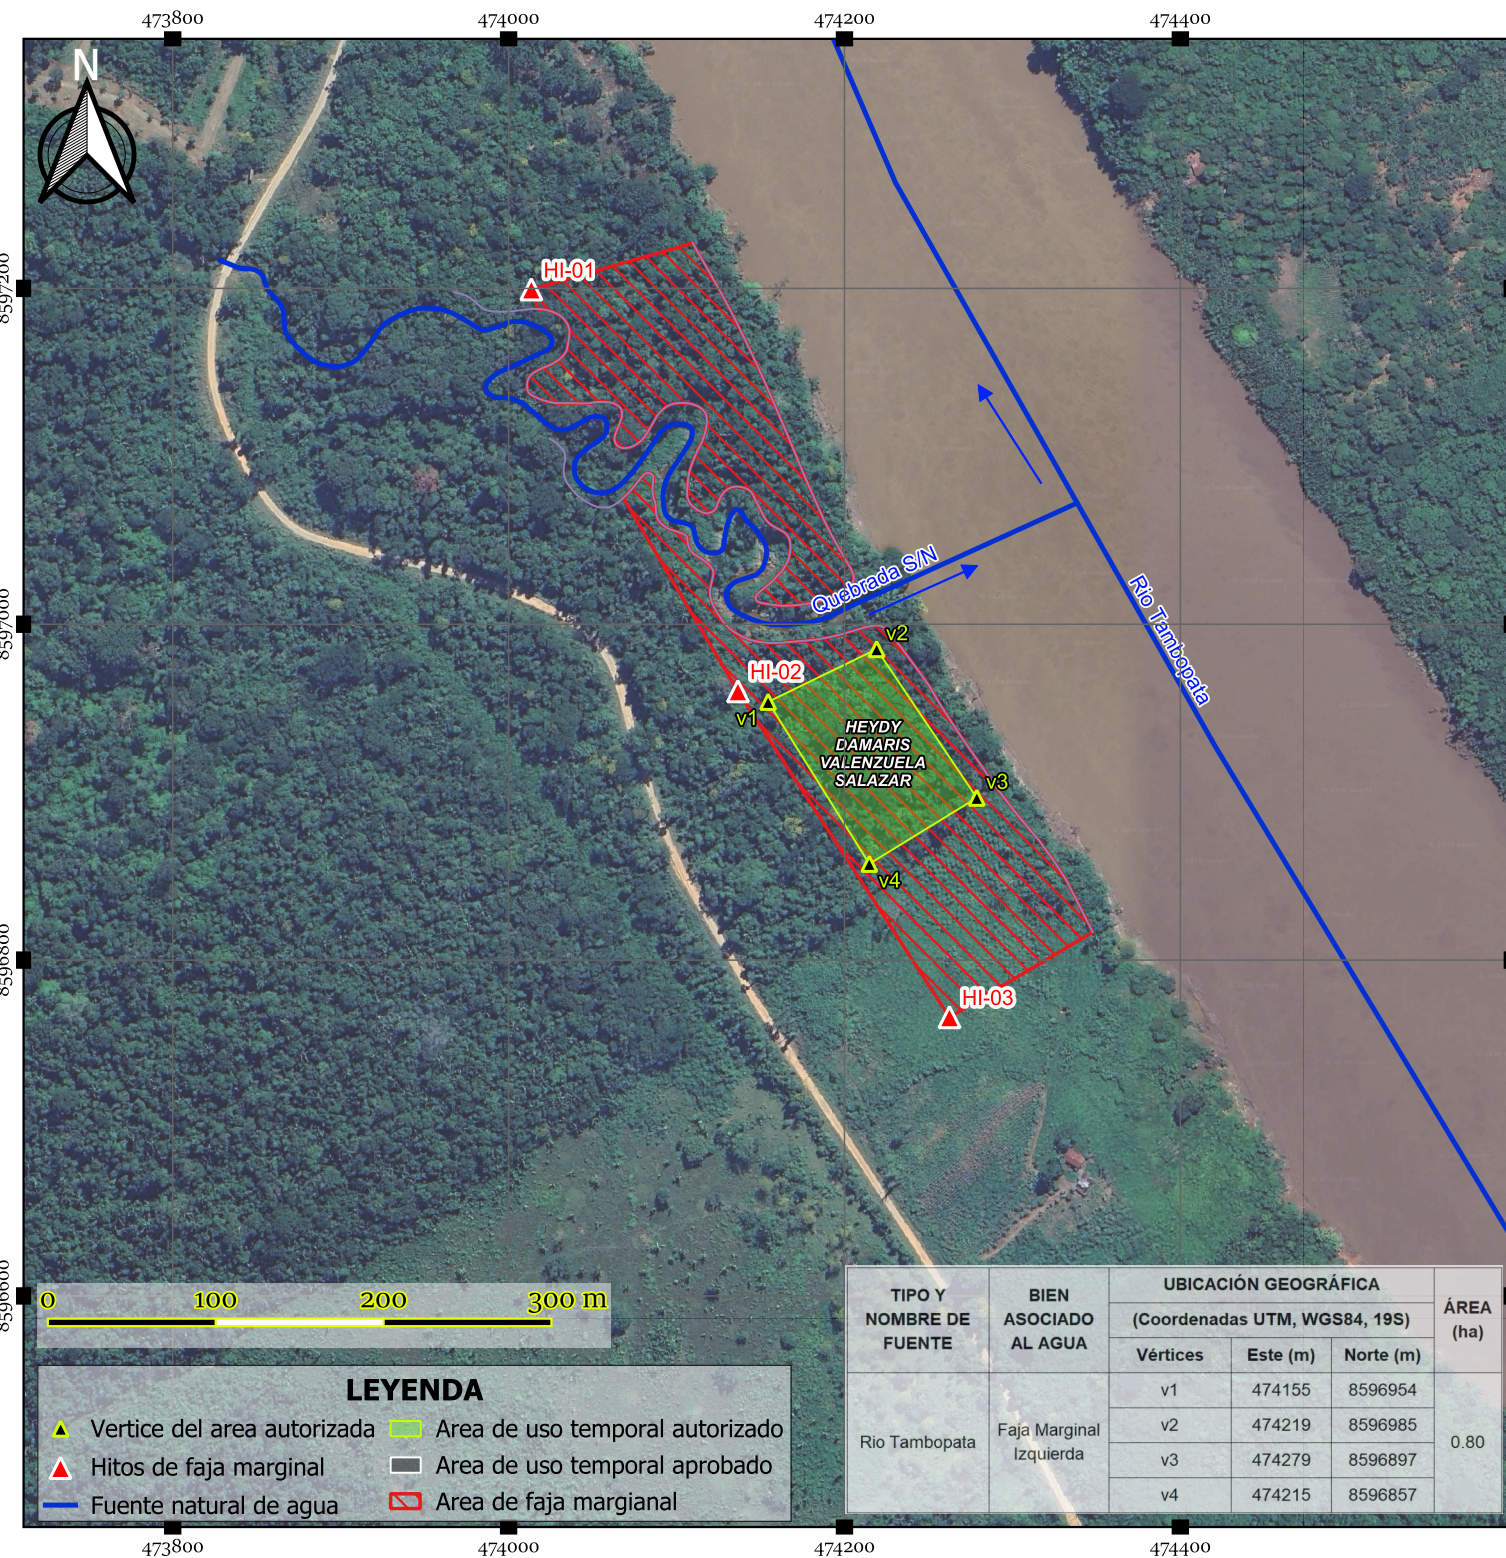

Titular : HEYDY DAMARIS VALENZUELA SALAZAR, con DNI N° 43549278

Proyecto : AUTORIZACIÓN DE USO TEMPORAL DE TERRENO DE LA FAJA MARGINAL IZQUIERDA DEL RÍO TAMBOPATA, PARA SIEMBRA DE CULTIVOS

Procedimiento : AUTORIZACION PARA EL USO TEMPORAL DE LAS FAJAS MARGINALES Y DE LAS RIBERAS DE LOS RIOS AMAZONICOS PARA LA SIEMBRA DE CULTIVOS

Codigo Unico de Tramite - CUT : 110483-2026

Escala : 1 : 4 500

Fecha : Julio 2026

Proyeccion Universal Transverse Mercator

Datum Horizontal : WGS 84

Datum Vertical : Nivel Medio del Mar

Zona : 19 Sur

Firmado digitalmente por MAMANI PACOMPIA Hipolito FAU 20520711865 hard Motivo: Doy V B

TIPO Y NOMBRE DE FUENTE	BIEN ASOCIADO AL AGUA	UBICACIÓN GEOGRÁFICA			ÁREA (ha)
		(Coordenadas UTM, WGS84, 19S)			
		Vértices	Este (m)	Norte (m)	
Rio Tambopata	Faja Marginal Izquierda	v1	474155	8596954	0.80
		v2	474219	8596985	
		v3	474279	8596897	
		v4	474215	8596857	

LEYENDA

- Vertice del area autorizada
- Hitos de faja marginal
- Fuente natural de agua
- Area de uso temporal autorizado
- Area de uso temporal aprobado
- Area de faja marginal