
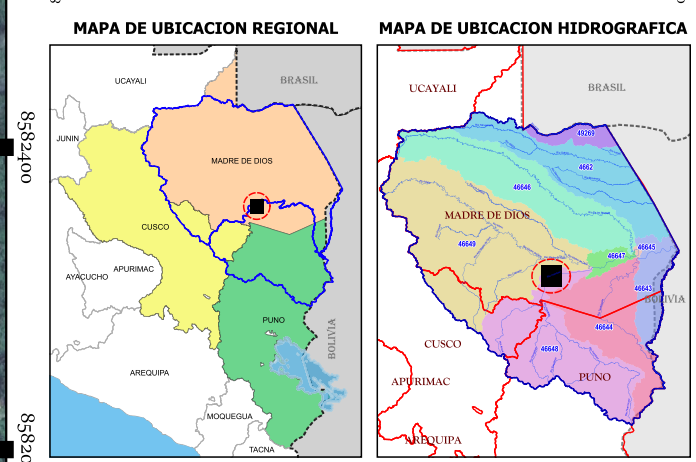
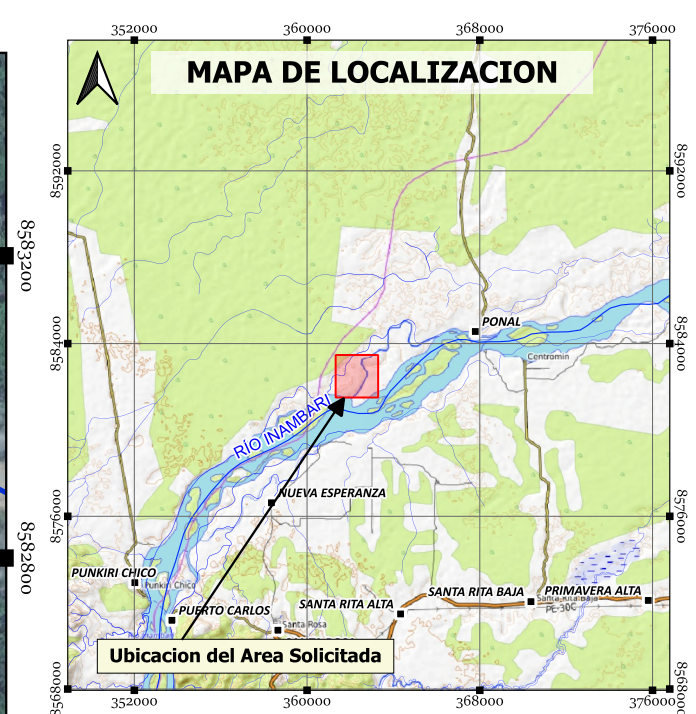


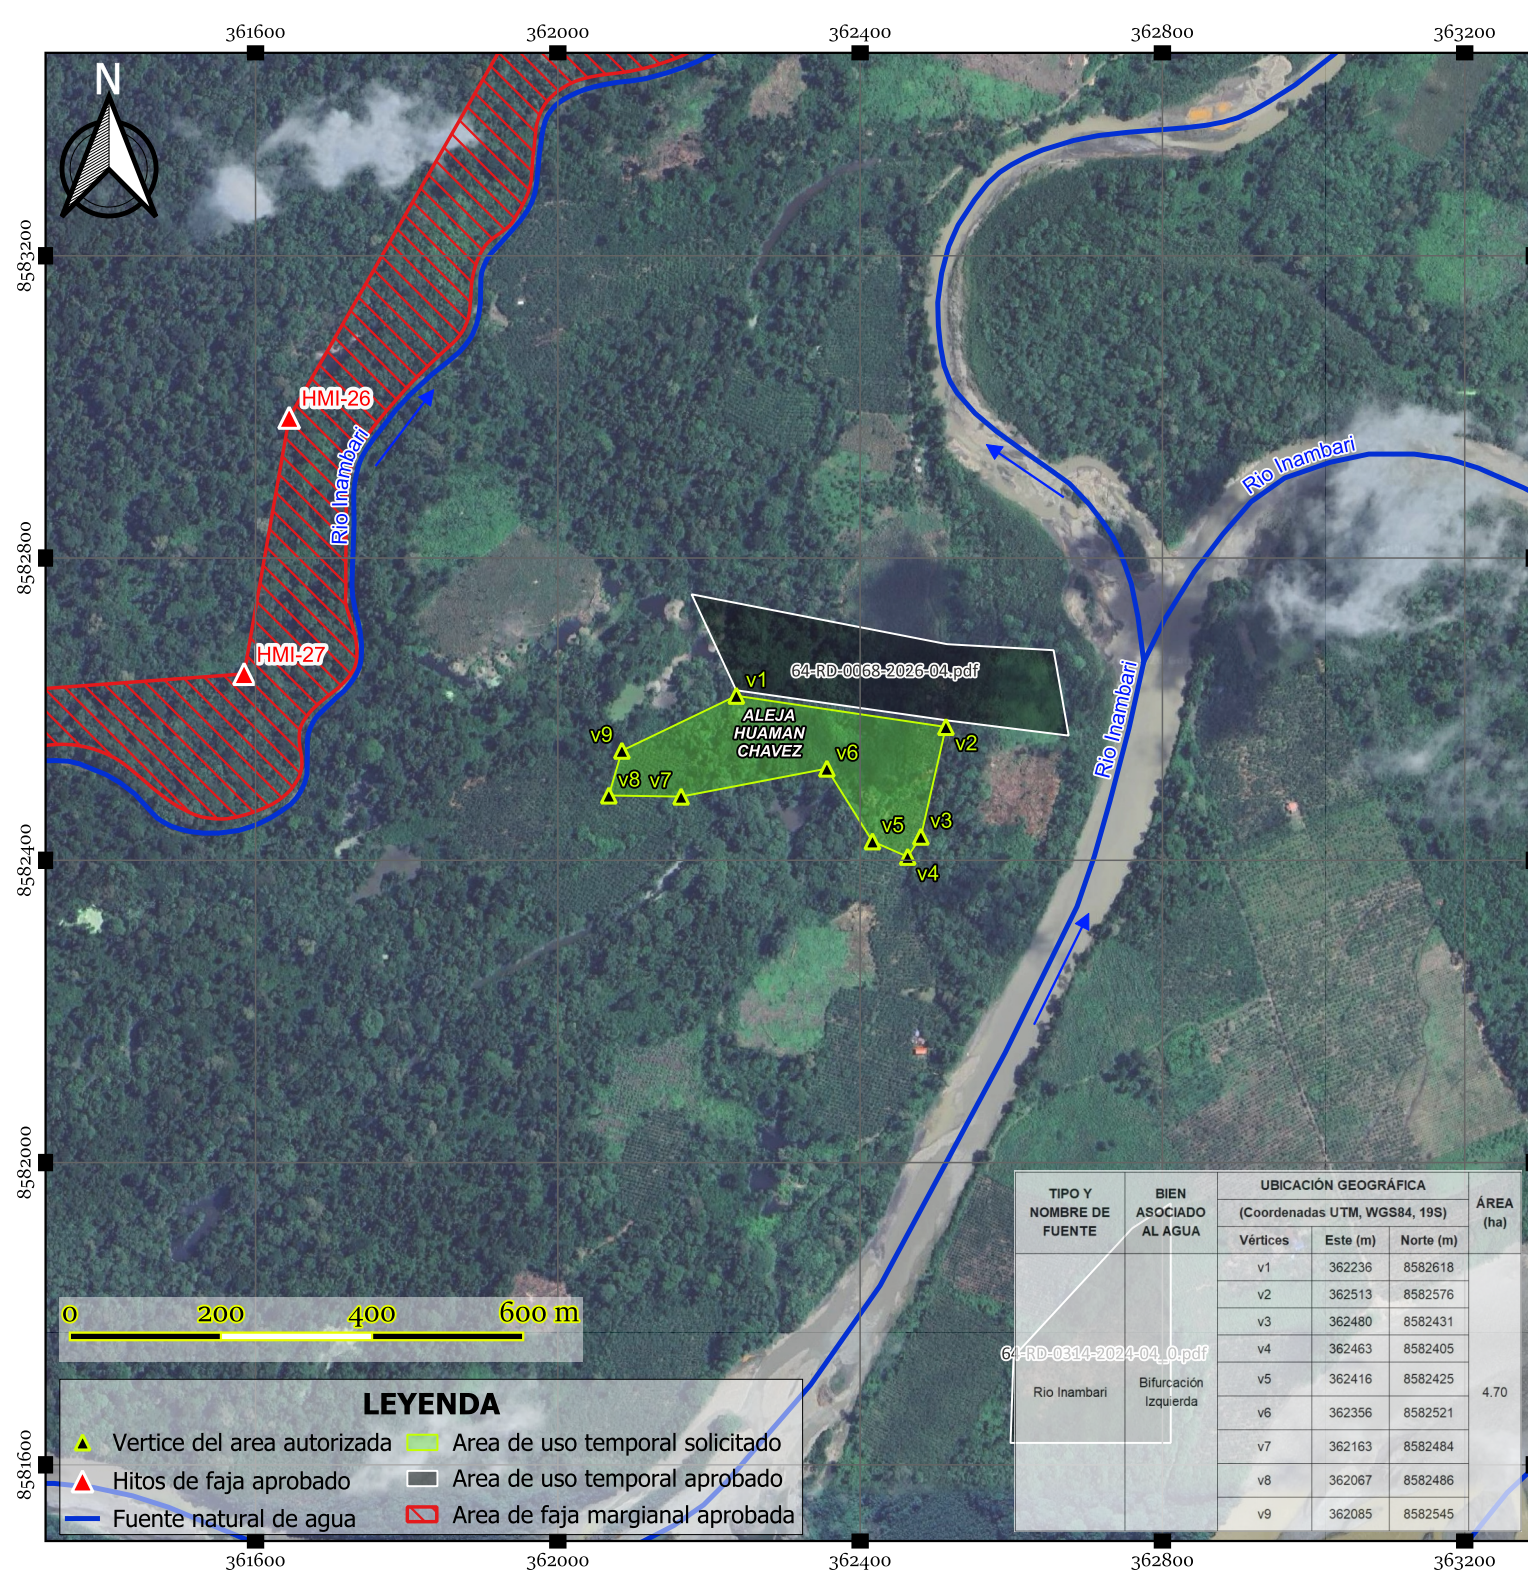

Ministerio de Desarrollo Agrario y Riego
ANA
Autoridad Nacional del Agua

Titular : ALEJA HUAMAN CHAVEZ, con DNI N° 24488309

Proyecto : AUTORIZACIÓN DE USO TEMPORAL DE TERRENO DE LA BIFURCACION IZQUIERDA DEL RÍO INAMBARÍ, PARA SIEMBRA DE CULTIVOS

Procedimiento : AUTORIZACION PARA EL USO TEMPORAL DE LAS FAJAS MARGINALES Y DE LAS RIBERAS DE LOS RIOS AMAZONICOS PARA LA SIEMBRA DE CULTIVOS

Código Único de Trámite - CUT : 81746-2026
Escala : 1 : 10 000
Fecha : Junio 2026
Proyección Universal Transverse Mercator
Datum Horizontal : WGS 84
Datum Vertical : Nivel Medio del Mar
Zona : 19 Sur

Firmado digitalmente por HUARANCA VILLASANTE Alex Juvenal FAU 30520711865 hgd Motivo: Day V 5

TIPO Y NOMBRE DE FUENTE	BIEN ASOCIADO AL AGUA	UBICACIÓN GEOGRÁFICA (Coordenadas UTM, WGS84, 19S)			ÁREA (ha)
		Vértices	Este (m)	Norte (m)	
Rio Inambari	Bifurcación Izquierda	v1	362236	8582618	4.70
		v2	362513	8582576	
		v3	362480	8582431	
		v4	362463	8582405	
		v5	362416	8582425	
		v6	362356	8582521	
		v7	362163	8582484	
		v8	362067	8582486	
		v9	362085	8582545	

LEYENDA

▲ Vertice del area autorizada ■ Area de uso temporal solicitado

▲ Hitos de faja aprobado ■ Area de uso temporal aprobado

— Fuente natural de agua ■ Area de faja marginal aprobada