



UBICACION DEPARTAMENTAL

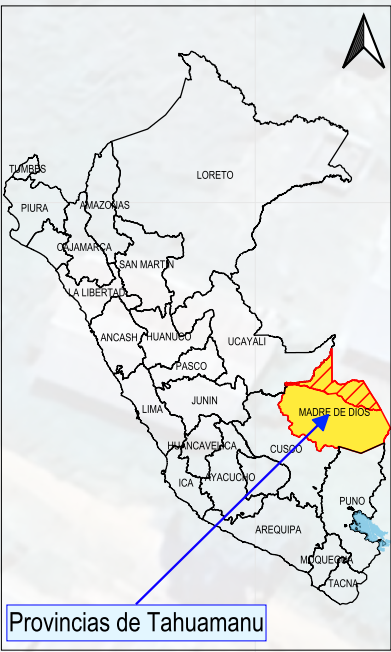

UBICACION PROVINCIAL

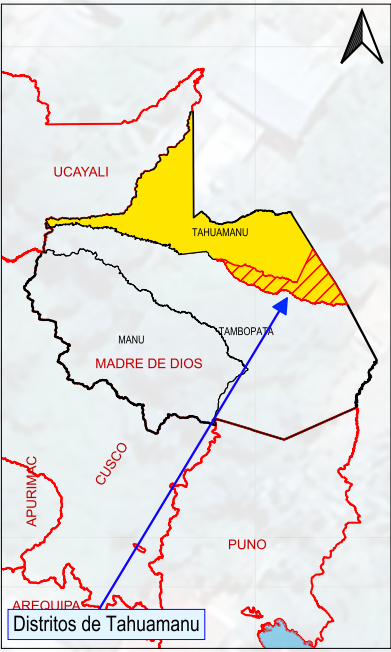

LEYENDA

- Hitos de señalizacion
- Progresiva
- Vertice de limite superior de ribera
- Eje de quebrada
- Limite superior de faja marginal
- Limite superior de la ribera
- Area de faja marginal

QUEBRADA 28 DE JULIO							
Proyeccion UTM-Datum WGS 84 - Zona 19 Sur							
Progresiva	LIMITE SUPERIOR DE LA RIBERA			VERTICE EXTERNO DE LA FAJA MARGINAL			
	VERTICE	ESTE (m)	NORTE (m)	Codigo del HITO	ESTE (m)	NORTE (m)	ANCHO DE FAJA MARGINAL (m)
0+002	1	485428	8687955	HD-01	485428	8687963	7
0+010	2	485418	8687957	HD-02	485416	8687964	7
0+087	3	485349	8687922	HD-03	485346	8687928	6
0+132	4	485315	8687890	HD-04	485310	8687897	9
0+192	5	485271	8687857	HD-05	485267	8687862	7
0+226	6	485246	8687831	HD-06	485240	8687836	8
0+263	7	485225	8687802	HD-07	485220	8687806	7

QUEBRADA 28 DE JULIO							
Proyeccion UTM-Datum WGS 84 - Zona 19 Sur							
Progresiva	LIMITE SUPERIOR DE LA RIBERA			VERTICE EXTERNO DE LA FAJA MARGINAL			
	VERTICE	ESTE (m)	NORTE (m)	Codigo del HITO	ESTE (m)	NORTE (m)	ANCHO DE FAJA MARGINAL (m)
0+001	1	485427	8687951	HI-01	485425	8687945	6
0+035	2	485400	8687935	HI-02	485403	8687929	6
0+075	3	485366	8687917	HI-03	485370	8687913	6
0+097	4	485356	8687898	HI-04	485360	8687894	6
0+117	5	485338	8687888	HI-05	485343	8687884	6
0+170	6	485305	8687857	HI-06	485309	8687854	5
0+215	7	485276	8687820	HI-07	485281	8687814	7
0+237	8	485259	8687809	HI-08	485263	8687804	6
0+262	9	485242	8687788	HI-09	485247	8687785	6



PERÚ

Ministerio de Desarrollo Agrario y Riego



ANA

Autoridad Nacional del Agua

AUTORIDAD NACIONAL DEL AGUA
Autoridad Administrativa del Agua Madre de Dios

"DELIMITACIÓN DE LA FAJA MARGINAL DE LA QUEBRADA 28 DE JULIO, EN EL SECTOR NUEVO SAN MARTIN, UBICADO EN EL DISTRITO Y PROVINCIA DE TAHUAMANU, DEPARTAMENTO MADRE DE DIOS"

P-01
Codigo Unico de Tramite - CUT : 98479-2026
Escala : 1 : 700
Fecha : Setiembre 2026
Proyeccion Universal Transvase Mercator
Datum Horizontal: WGS-84
Datum Vertical: Nivel Medio del Mar
Zona: 19 Sur

Firmado digitalmente por MAMANI PACOMPIA Hipolito FAU 20520711865 hard Motivo: Doy V° B°

