


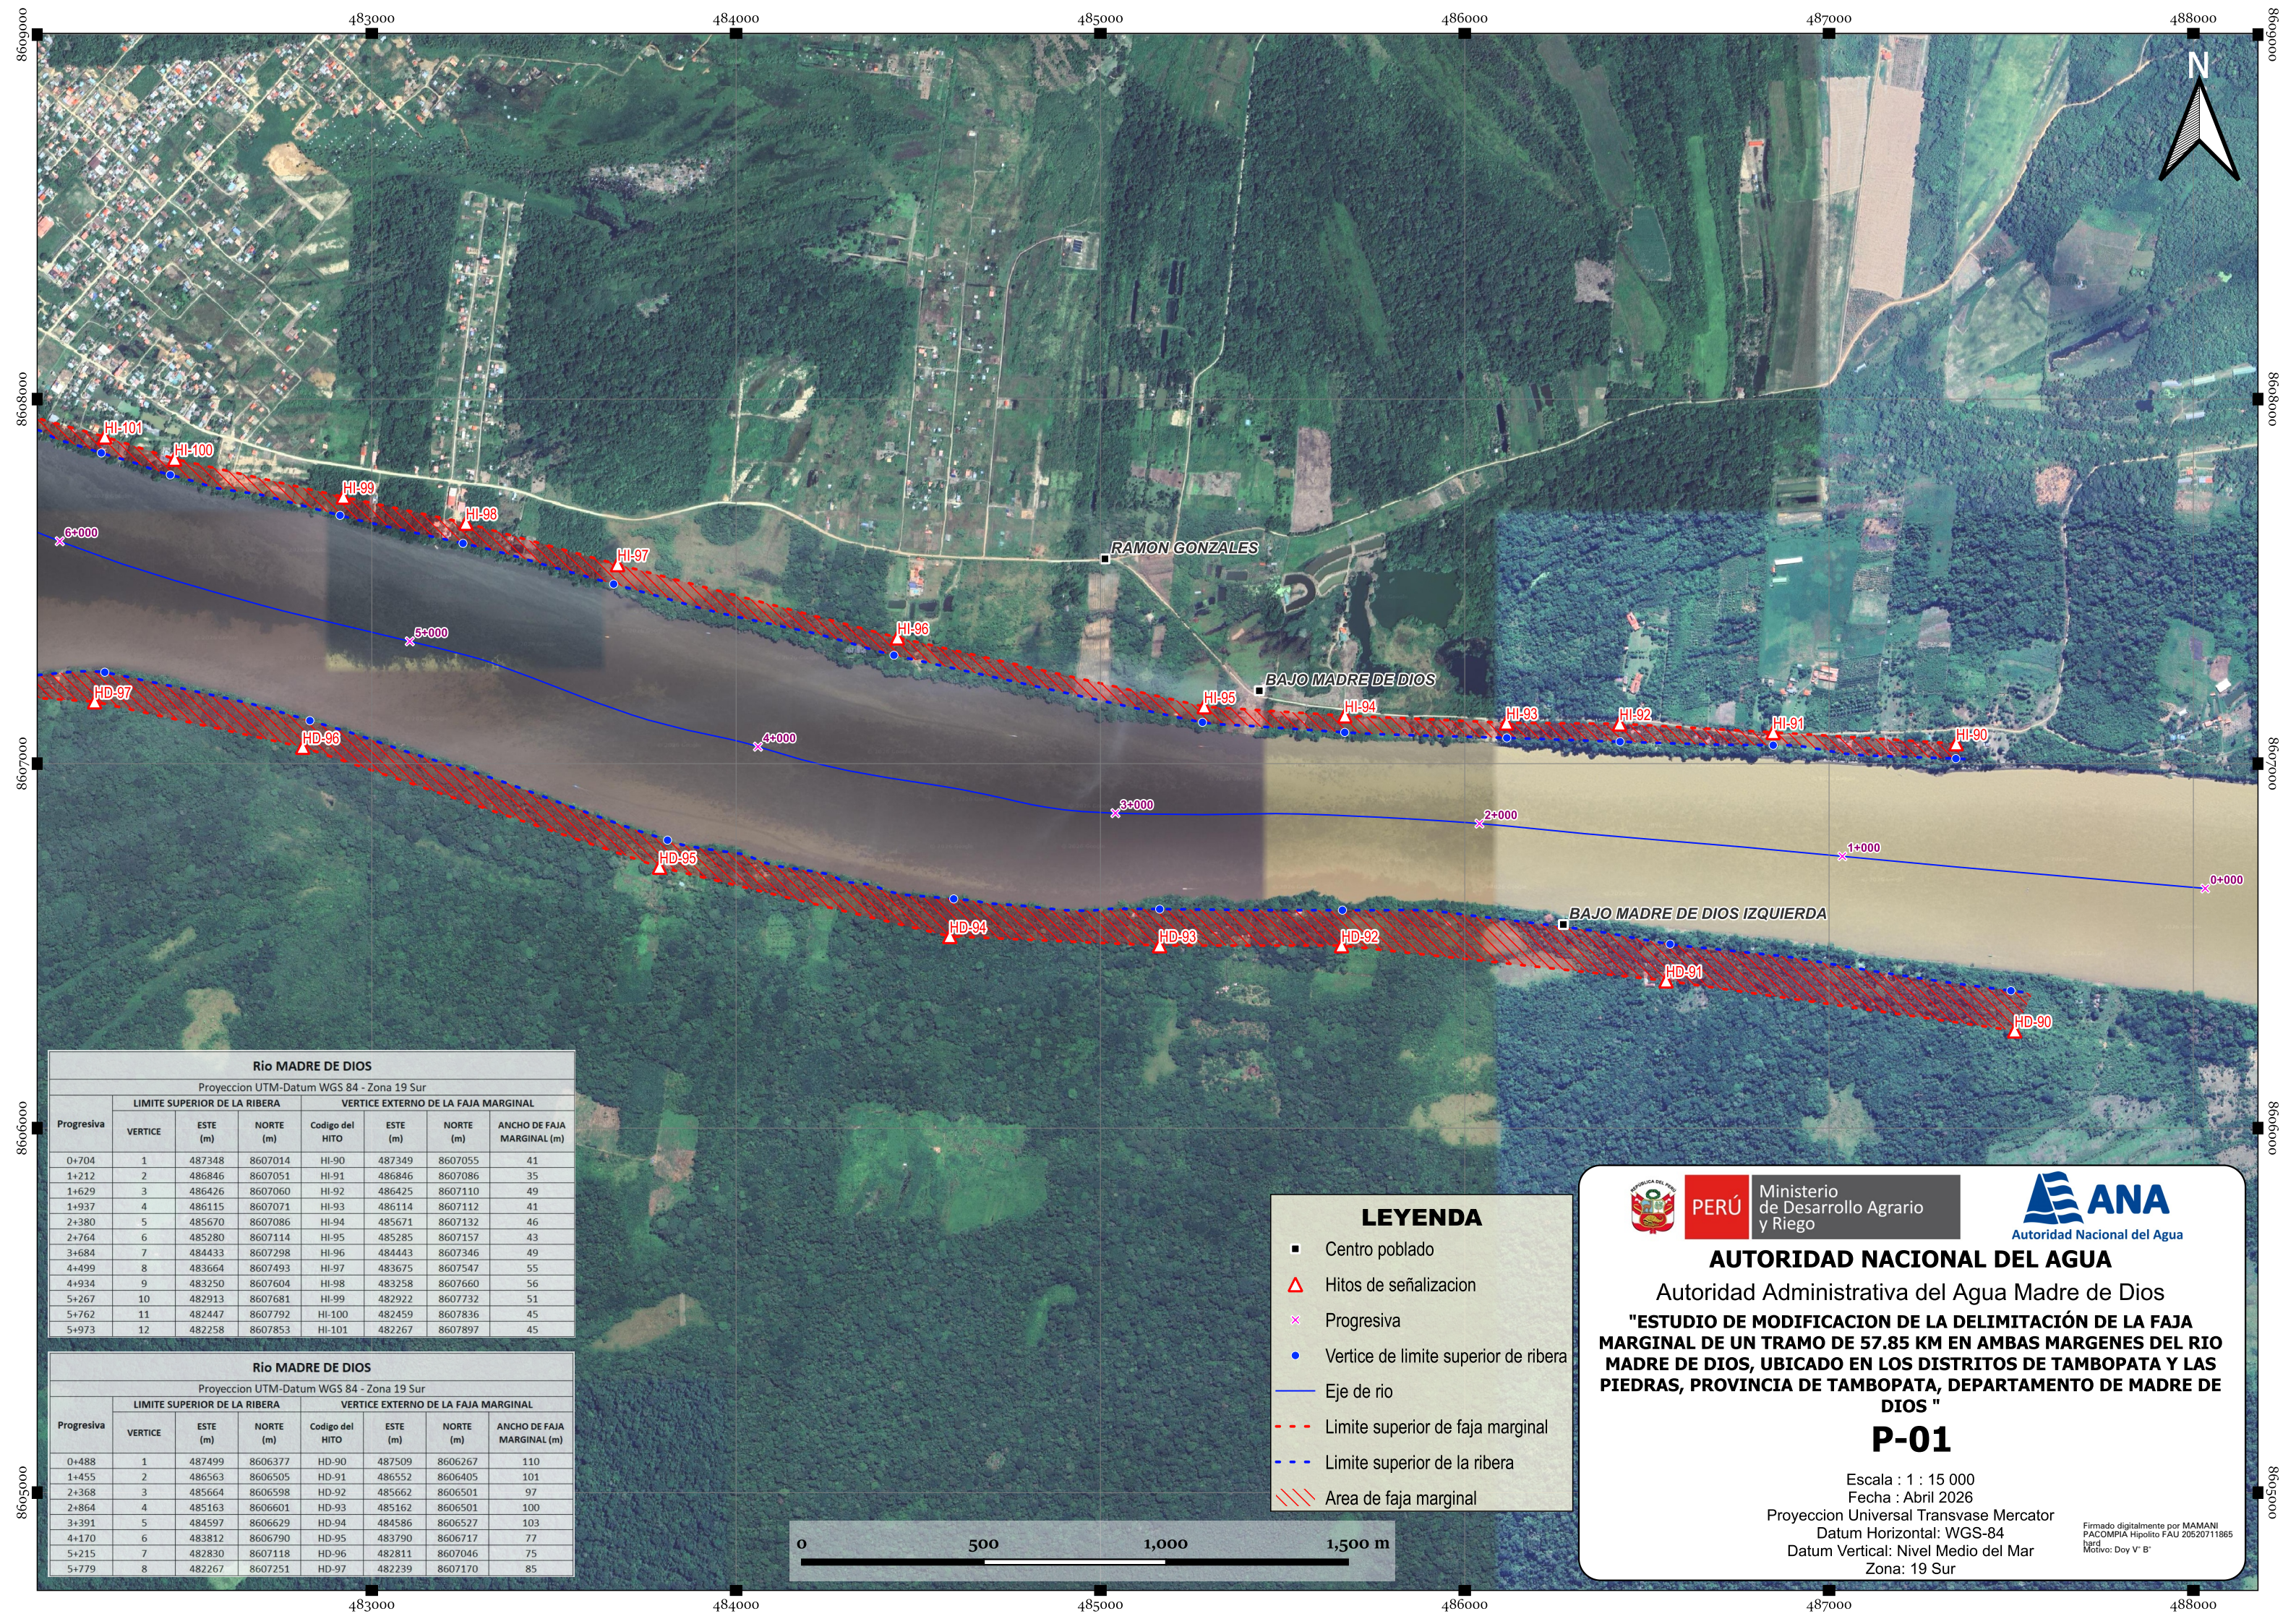

Río MADRE DE DIOS							
Proyeccion UTM-Datum WGS 84 - Zona 19 Sur							
Progresiva	LIMITE SUPERIOR DE LA RIBERA			VERTICE EXTERNO DE LA FAJA MARGINAL			
	VERTICE	ESTE (m)	NORTE (m)	Codigo del HITO	ESTE (m)	NORTE (m)	ANCHO DE FAJA MARGINAL (m)
0+704	1	487348	8607014	HI-90	487349	8607055	41
1+212	2	486846	8607051	HI-91	486846	8607086	35
1+629	3	486426	8607060	HI-92	486425	8607110	49
1+937	4	486115	8607071	HI-93	486114	8607112	41
2+380	5	485670	8607086	HI-94	485671	8607132	46
2+764	6	485280	8607114	HI-95	485285	8607157	43
3+684	7	484433	8607298	HI-96	484443	8607346	49
4+499	8	483664	8607493	HI-97	483675	8607547	55
4+934	9	483250	8607604	HI-98	483258	8607660	56
5+267	10	482913	8607681	HI-99	482922	8607732	51
5+762	11	482447	8607792	HI-100	482459	8607836	45
5+973	12	482258	8607853	HI-101	482267	8607897	45

Río MADRE DE DIOS							
Proyeccion UTM-Datum WGS 84 - Zona 19 Sur							
Progresiva	LIMITE SUPERIOR DE LA RIBERA			VERTICE EXTERNO DE LA FAJA MARGINAL			
	VERTICE	ESTE (m)	NORTE (m)	Codigo del HITO	ESTE (m)	NORTE (m)	ANCHO DE FAJA MARGINAL (m)
0+488	1	487499	8606377	HD-90	487509	8606267	110
1+455	2	486563	8606505	HD-91	486552	8606405	101
2+368	3	485664	8606598	HD-92	485662	8606501	97
2+864	4	485163	8606601	HD-93	485162	8606501	100
3+391	5	484597	8606629	HD-94	484586	8606527	103
4+170	6	483812	8606790	HD-95	483790	8606717	77
5+215	7	482830	8607118	HD-96	482811	8607046	75
5+779	8	482267	8607251	HD-97	482239	8607170	85

LEYENDA

■

 Centro poblado

▲

 Hitos de señalizacion

×

 Progresiva

●

 Vertice de limite superior de ribera

—

 Eje de rio

- - -

 Limite superior de faja marginal

- - -

 Limite superior de la ribera

////

 Area de faja marginal

PERÚ

Ministerio de Desarrollo Agrario y Riego

AUTORIDAD NACIONAL DEL AGUA

Autoridad Administrativa del Agua Madre de Dios

"ESTUDIO DE MODIFICACION DE LA DELIMITACIÓN DE LA FAJA MARGINAL DE UN TRAMO DE 57.85 KM EN AMBAS MARGENES DEL RIO MADRE DE DIOS, UBICADO EN LOS DISTRITOS DE TAMBOPATA Y LAS PIEDRAS, PROVINCIA DE TAMBOPATA, DEPARTAMENTO DE MADRE DE DIOS "

P-01

Escala : 1 : 15 000

Fecha : Abril 2026

Proyeccion Universal Transvase Mercator

Datum Horizontal: WGS-84

Datum Vertical: Nivel Medio del Mar

Zona: 19 Sur

Firmado digitalmente por MAMANI PACOMPIA Hipolito FAU 20520711865
hard
Motivo: Doy V° B°