


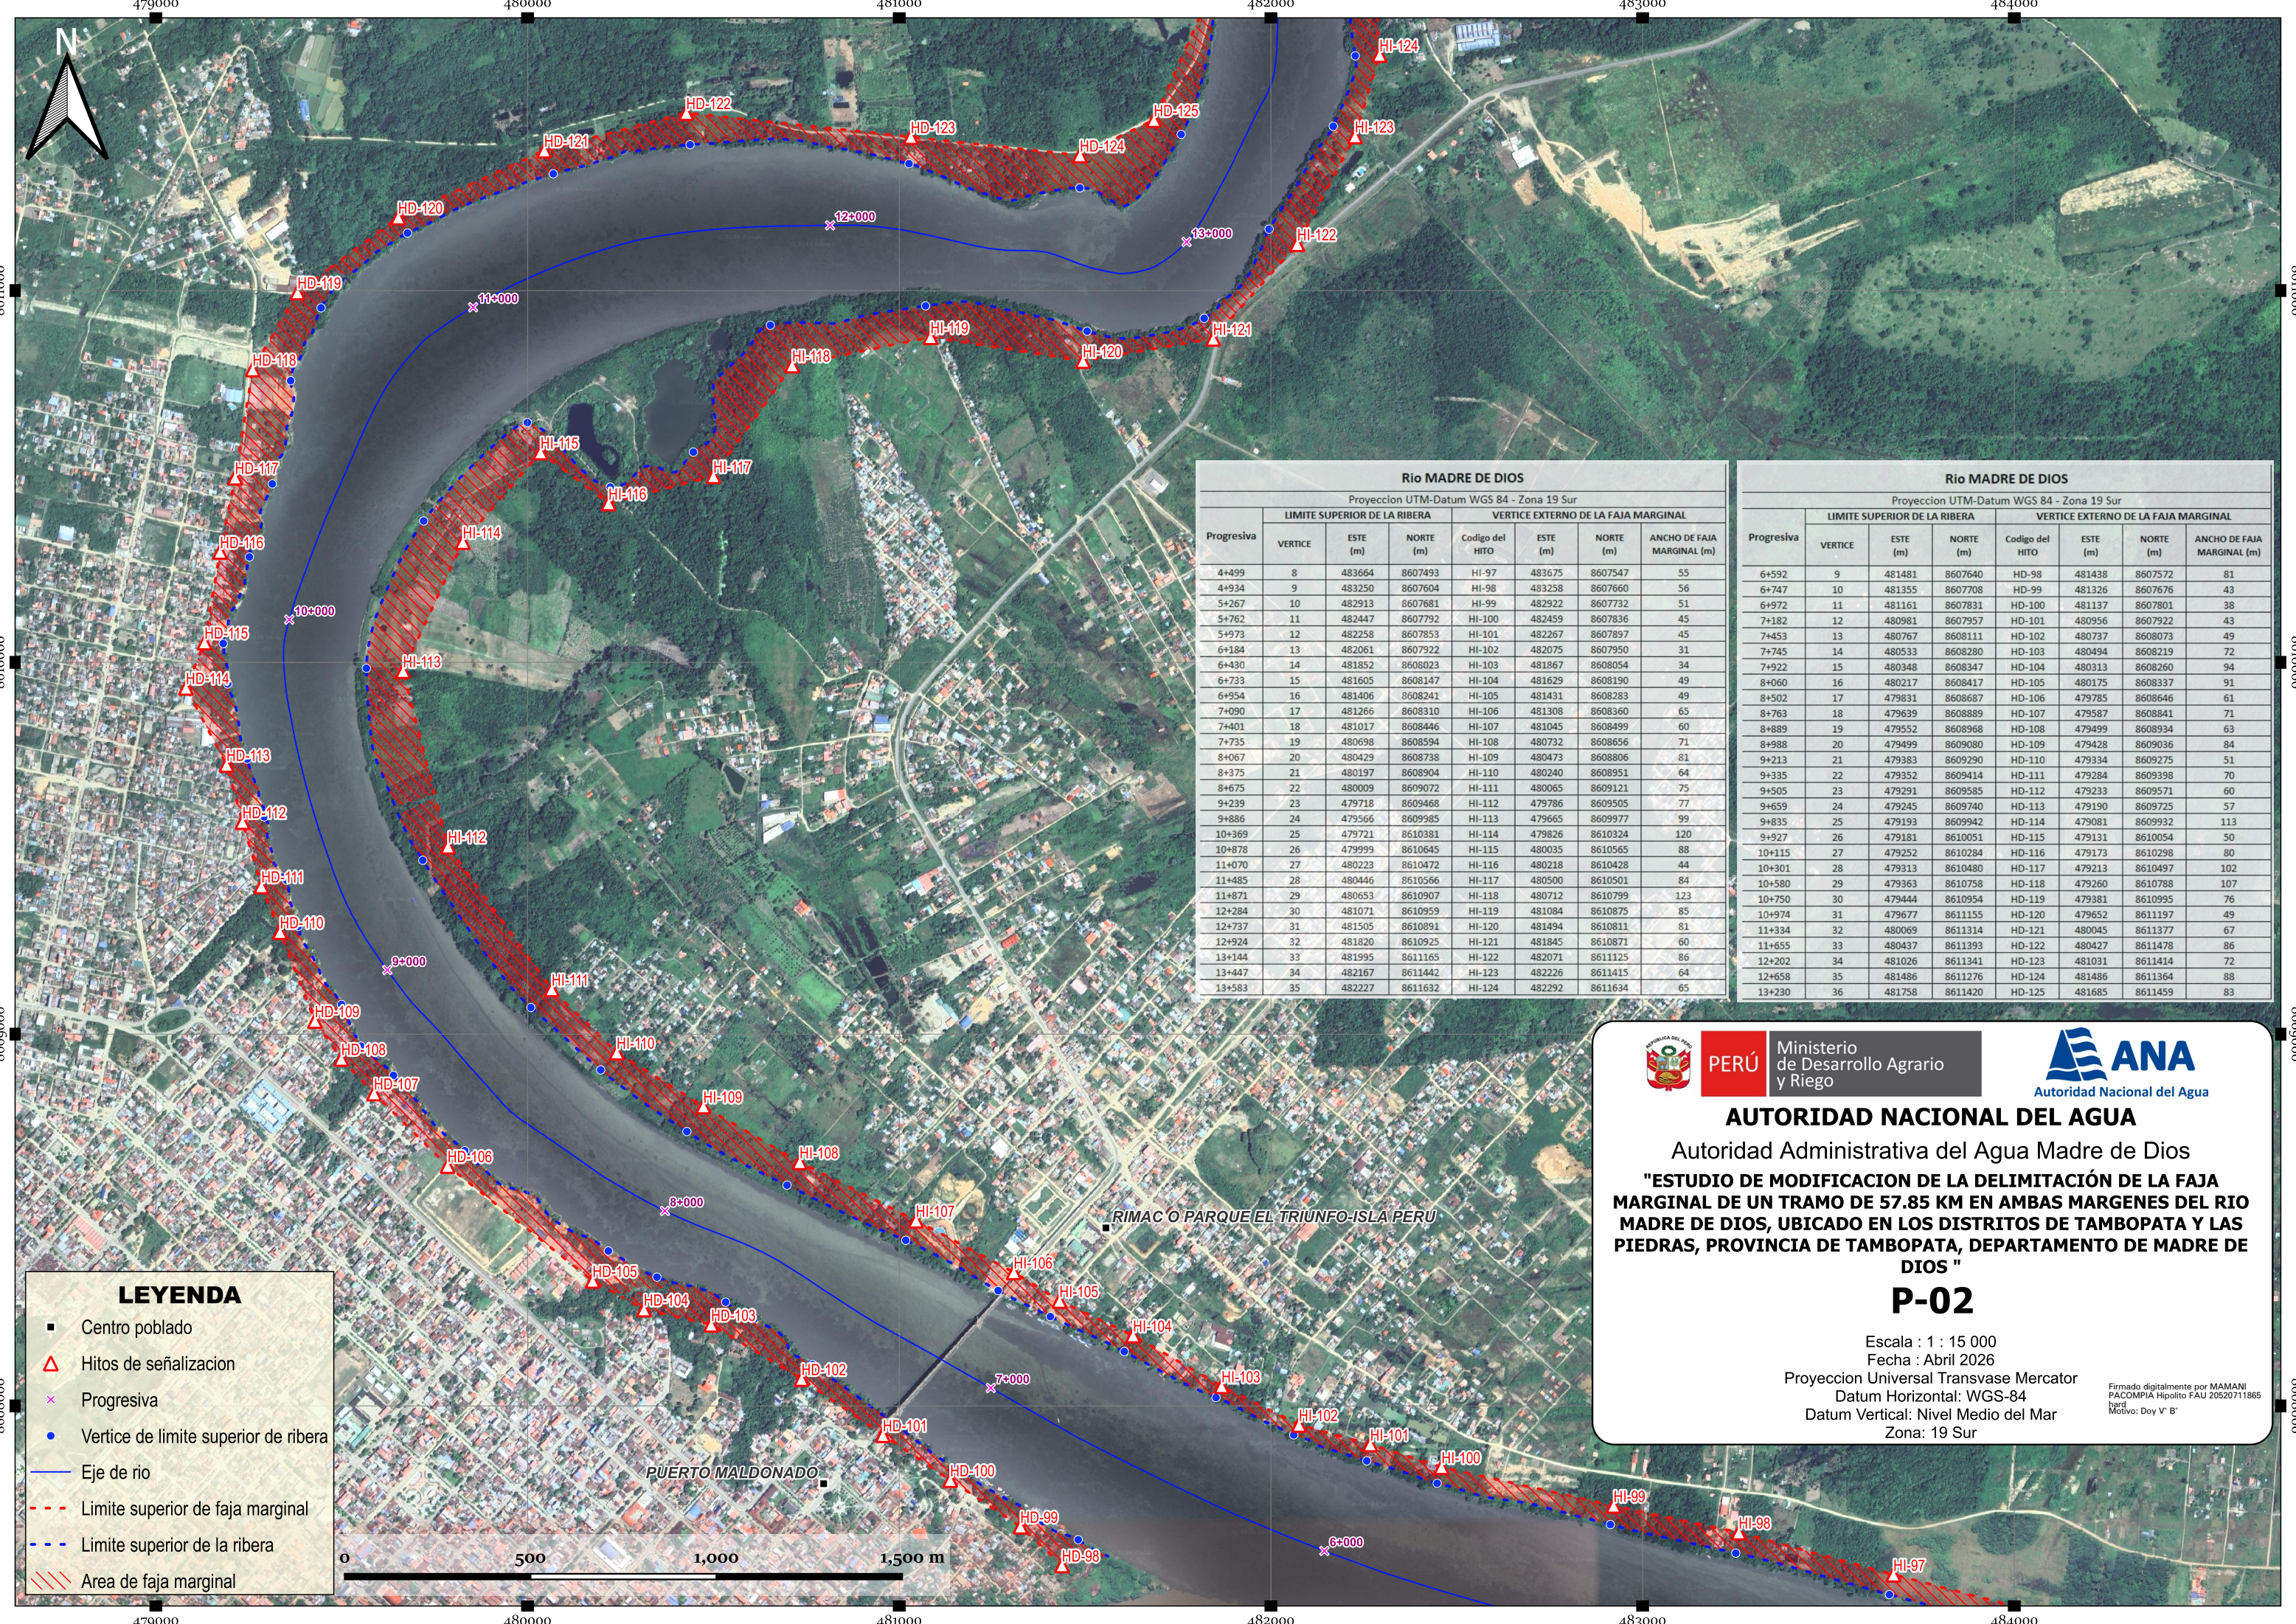

Rio MADRE DE DIOS							
Proyeccion UTM-Datum WGS 84 - Zona 19 Sur							
Progresiva	LIMITE SUPERIOR DE LA RIBERA			VERTICE EXTERNO DE LA FAJA MARGINAL			
	VERTICE	ESTE (m)	NORTE (m)	Codigo del HITO	ESTE (m)	NORTE (m)	ANCHO DE FAJA MARGINAL (m)
4+499	8	483664	8607493	HI-97	483675	8607547	55
4+934	9	483250	8607604	HI-98	483258	8607660	56
5+267	10	482913	8607681	HI-99	482922	8607732	51
5+762	11	482447	8607792	HI-100	482459	8607836	45
5+973	12	482258	8607853	HI-101	482267	8607897	45
6+184	13	482061	8607922	HI-102	482075	8607950	31
6+430	14	481852	8608023	HI-103	481867	8608054	34
6+733	15	481605	8608147	HI-104	481629	8608190	49
6+954	16	481406	8608241	HI-105	481431	8608283	49
7+090	17	481266	8608310	HI-106	481308	8608360	65
7+401	18	481017	8608446	HI-107	481045	8608499	60
7+735	19	480698	8608594	HI-108	480732	8608656	71
8+067	20	480429	8608738	HI-109	480473	8608806	81
8+375	21	480197	8608904	HI-110	480240	8608951	64
8+675	22	480009	8609072	HI-111	480065	8609121	75
9+239	23	479718	8609468	HI-112	479786	8609505	77
9+886	24	479566	8609985	HI-113	479665	8609977	99
10+369	25	479721	8610381	HI-114	479826	8610324	120
10+878	26	479999	8610645	HI-115	480035	8610565	88
11+070	27	480223	8610472	HI-116	480218	8610428	44
11+485	28	480446	8610566	HI-117	480500	8610501	84
11+871	29	480653	8610907	HI-118	480712	8610799	123
12+284	30	481071	8610959	HI-119	481084	8610875	85
12+737	31	481505	8610891	HI-120	481494	8610811	81
12+924	32	481820	8610925	HI-121	481845	8610871	60
13+144	33	481995	8611165	HI-122	482071	8611125	86
13+447	34	482167	8611442	HI-123	482226	8611415	64
13+583	35	482227	8611632	HI-124	482292	8611634	65

Rio MADRE DE DIOS							
Proyeccion UTM-Datum WGS 84 - Zona 19 Sur							
Progresiva	LIMITE SUPERIOR DE LA RIBERA			VERTICE EXTERNO DE LA FAJA MARGINAL			
	VERTICE	ESTE (m)	NORTE (m)	Codigo del HITO	ESTE (m)	NORTE (m)	ANCHO DE FAJA MARGINAL (m)
6+592	9	481481	8607640	HD-98	481438	8607572	81
6+747	10	481355	8607708	HD-99	481326	8607676	43
6+972	11	481161	8607831	HD-100	481137	8607801	38
7+182	12	480981	8607957	HD-101	480956	8607922	43
7+453	13	480767	8608111	HD-102	480737	8608073	49
7+745	14	480533	8608280	HD-103	480494	8608219	72
7+922	15	480348	8608347	HD-104	480313	8608260	94
8+060	16	480217	8608417	HD-105	480175	8608337	91
8+502	17	479831	8608687	HD-106	479785	8608646	61
8+763	18	479639	8608889	HD-107	479587	8608841	71
8+889	19	479552	8608968	HD-108	479499	8608934	63
8+988	20	479499	8609080	HD-109	479428	8609036	84
9+213	21	479383	8609290	HD-110	479334	8609275	51
9+335	22	479352	8609414	HD-111	479284	8609398	70
9+505	23	479291	8609585	HD-112	479233	8609571	60
9+659	24	479245	8609740	HD-113	479190	8609725	57
9+835	25	479193	8609942	HD-114	479081	8609932	113
9+927	26	479181	8610051	HD-115	479131	8610054	50
10+115	27	479252	8610284	HD-116	479173	8610298	80
10+301	28	479313	8610480	HD-117	479213	8610497	102
10+580	29	479363	8610758	HD-118	479260	8610788	107
10+750	30	479444	8610954	HD-119	479381	8610995	76
10+974	31	479677	8611155	HD-120	479652	8611197	49
11+334	32	480069	8611314	HD-121	480045	8611377	67
11+655	33	480437	8611393	HD-122	480427	8611478	86
12+202	34	481026	8611341	HD-123	481031	8611414	72
12+658	35	481486	8611276	HD-124	481486	8611364	88
13+230	36	481758	8611420	HD-125	481685	8611459	83

LEYENDA

■

Centro poblado

▲

Hitos de señalizacion

×

Progresiva

●

Vertice de limite superior de ribera

—

Eje de rio

- - -

Limite superior de faja marginal

- - -

Limite superior de la ribera

///

Area de faja marginal



PERÚ

Ministerio de Desarrollo Agrario y Riego



ANA

Autoridad Nacional del Agua

AUTORIDAD NACIONAL DEL AGUA

Autoridad Administrativa del Agua Madre de Dios

"ESTUDIO DE MODIFICACION DE LA DELIMITACIÓN DE LA FAJA MARGINAL DE UN TRAMO DE 57.85 KM EN AMBAS MARGENES DEL RIO MADRE DE DIOS, UBICADO EN LOS DISTRITOS DE TAMBOPATA Y LAS PIEDRAS, PROVINCIA DE TAMBOPATA, DEPARTAMENTO DE MADRE DE DIOS "

P-02

Escala : 1 : 15 000

Fecha : Abril 2026

Proyeccion Universal Transvase Mercator

Datum Horizontal: WGS-84

Datum Vertical: Nivel Medio del Mar

Zona: 19 Sur

Firmado digitalmente por MAMANI PACOMPIA Hipolito FAU 20520711865

hspd

Motivo: Doy V° B°