


Río MADRE DE DIOS							
Proyeccion UTM-Datum WGS 84 - Zona 19 Sur							
Progresiva	LIMITE SUPERIOR DE LA RIBERA			VERTICE EXTERNO DE LA FAJA MARGINAL			
	VERTICE	ESTE (m)	NORTE (m)	Codigo del HITO	ESTE (m)	NORTE (m)	ANCHO DE FAJA MARGINAL (m)
37+153	97	476755	8611836	HI-186	476699	8611806	63
37+679	98	476997	8611457	HI-187	476928	8611430	75
38+259	99	477192	8610945	HI-188	477137	8610933	56
38+930	100	477385	8610319	HI-189	477343	8610313	43
39+386	101	477452	8609909	HI-190	477386	8609922	67
39+593	102	477347	8609776	HI-191	477289	8609797	61
39+823	103	477351	8609561	HI-192	477295	8609592	64
40+188	104	477126	8609389	HI-193	477099	8609436	55
40+495	105	476875	8609307	HI-194	476859	8609359	54
40+840	106	476568	8609297	HI-195	476569	8609342	45
41+366	107	476117	8609386	HI-196	476125	8609446	60
41+960	108	475529	8609475	HI-197	475544	8609557	84
42+544	109	474966	8609613	HI-198	474977	8609670	58
42+899	110	474641	8609715	HI-199	474662	8609780	69
43+324	111	474265	8609862	HI-200	474278	8609908	48
43+654	112	473972	8609999	HI-201	473992	8610051	55
44+242	113	473439	8610203	HI-202	473460	8610259	60
44+593	114	473149	8610384	HI-203	473165	8610420	40
44+997	115	472698	8610592	HI-204	472714	8610641	52
45+185	116	472494	8610648	HI-205	472501	8610719	70

Río MADRE DE DIOS							
Proyeccion UTM-Datum WGS 84 - Zona 19 Sur							
Progresiva	LIMITE SUPERIOR DE LA RIBERA			VERTICE EXTERNO DE LA FAJA MARGINAL			
	VERTICE	ESTE (m)	NORTE (m)	Codigo del HITO	ESTE (m)	NORTE (m)	ANCHO DE FAJA MARGINAL (m)
37+260	96	477199	8612055	HD-185	477233	8612094	52
37+497	97	477342	8611848	HD-186	477378	8611880	48
37+621	98	477469	8611718	HD-187	477514	8611741	50
37+795	99	477527	8611533	HD-188	477567	8611558	47
37+882	100	477585	8611469	HD-189	477633	8611495	55
38+132	101	477651	8611208	HD-190	477703	8611211	52
38+601	102	477657	8610710	HD-191	477717	8610718	60
38+697	103	477689	8610622	HD-192	477716	8610630	28
38+781	104	477707	8610527	HD-193	477748	8610528	41
38+885	105	477702	8610412	HD-194	477726	8610415	24
38+975	106	477706	8610323	HD-195	477743	8610326	37
39+029	107	477715	8610268	HD-196	477743	8610274	29
39+187	108	477765	8610129	HD-197	477790	8610138	27
39+258	109	477782	8610033	HD-198	477808	8610042	28
39+341	110	477803	8609925	HD-199	477826	8609928	23
39+487	111	477781	8609756	HD-200	477827	8609752	46
39+573	112	477769	8609645	HD-201	477803	8609636	35
39+684	113	477728	8609530	HD-202	477757	8609517	32
39+844	114	477630	8609363	HD-203	477664	8609344	39
39+925	115	477575	8609296	HD-204	477600	8609274	33
40+027	116	477475	8609193	HD-205	477516	8609152	58
40+122	117	477379	8609116	HD-206	477407	8609078	47
40+260	118	477227	8609035	HD-207	477254	8608982	60
40+462	119	477016	8608932	HD-208	477031	8608901	34
40+687	120	476774	8608840	HD-209	476782	8608811	31
40+735	121	476734	8608838	HD-210	476736	8608781	57
40+867	122	476567	8608821	HD-211	476573	8608786	36
40+918	123	476495	8608791	HD-212	476498	8608758	34
40+978	124	476428	8608793	HD-213	476429	8608751	42
41+048	125	476339	8608804	HD-214	476330	8608752	52
41+158	126	476230	8608841	HD-215	476217	8608776	66
41+360	127	476028	8608874	HD-216	476016	8608818	57
41+592	128	475809	8608932	HD-217	475792	8608877	58
41+903	129	475509	8609054	HD-218	475489	8608984	73
42+185	130	475231	8609122	HD-219	475207	8609035	90
42+433	131	474978	8609186	HD-220	474960	8609112	76
42+705	132	474708	8609242	HD-221	474690	8609176	69
42+877	133	474531	8609285	HD-222	474515	8609228	59
43+188	134	474233	8609388	HD-223	474204	8609322	72
43+545	135	473884	8609544	HD-224	473865	8609498	50
43+905	136	473542	8609660	HD-225	473518	8609617	50
44+099	137	473379	8609754	HD-226	473335	8609721	55
44+159	138	473337	8609798	HD-227	473300	8609769	47
44+534	139	472989	8610007	HD-228	472964	8609965	49
44+915	140	472705	8610123	HD-229	472694	8610074	50

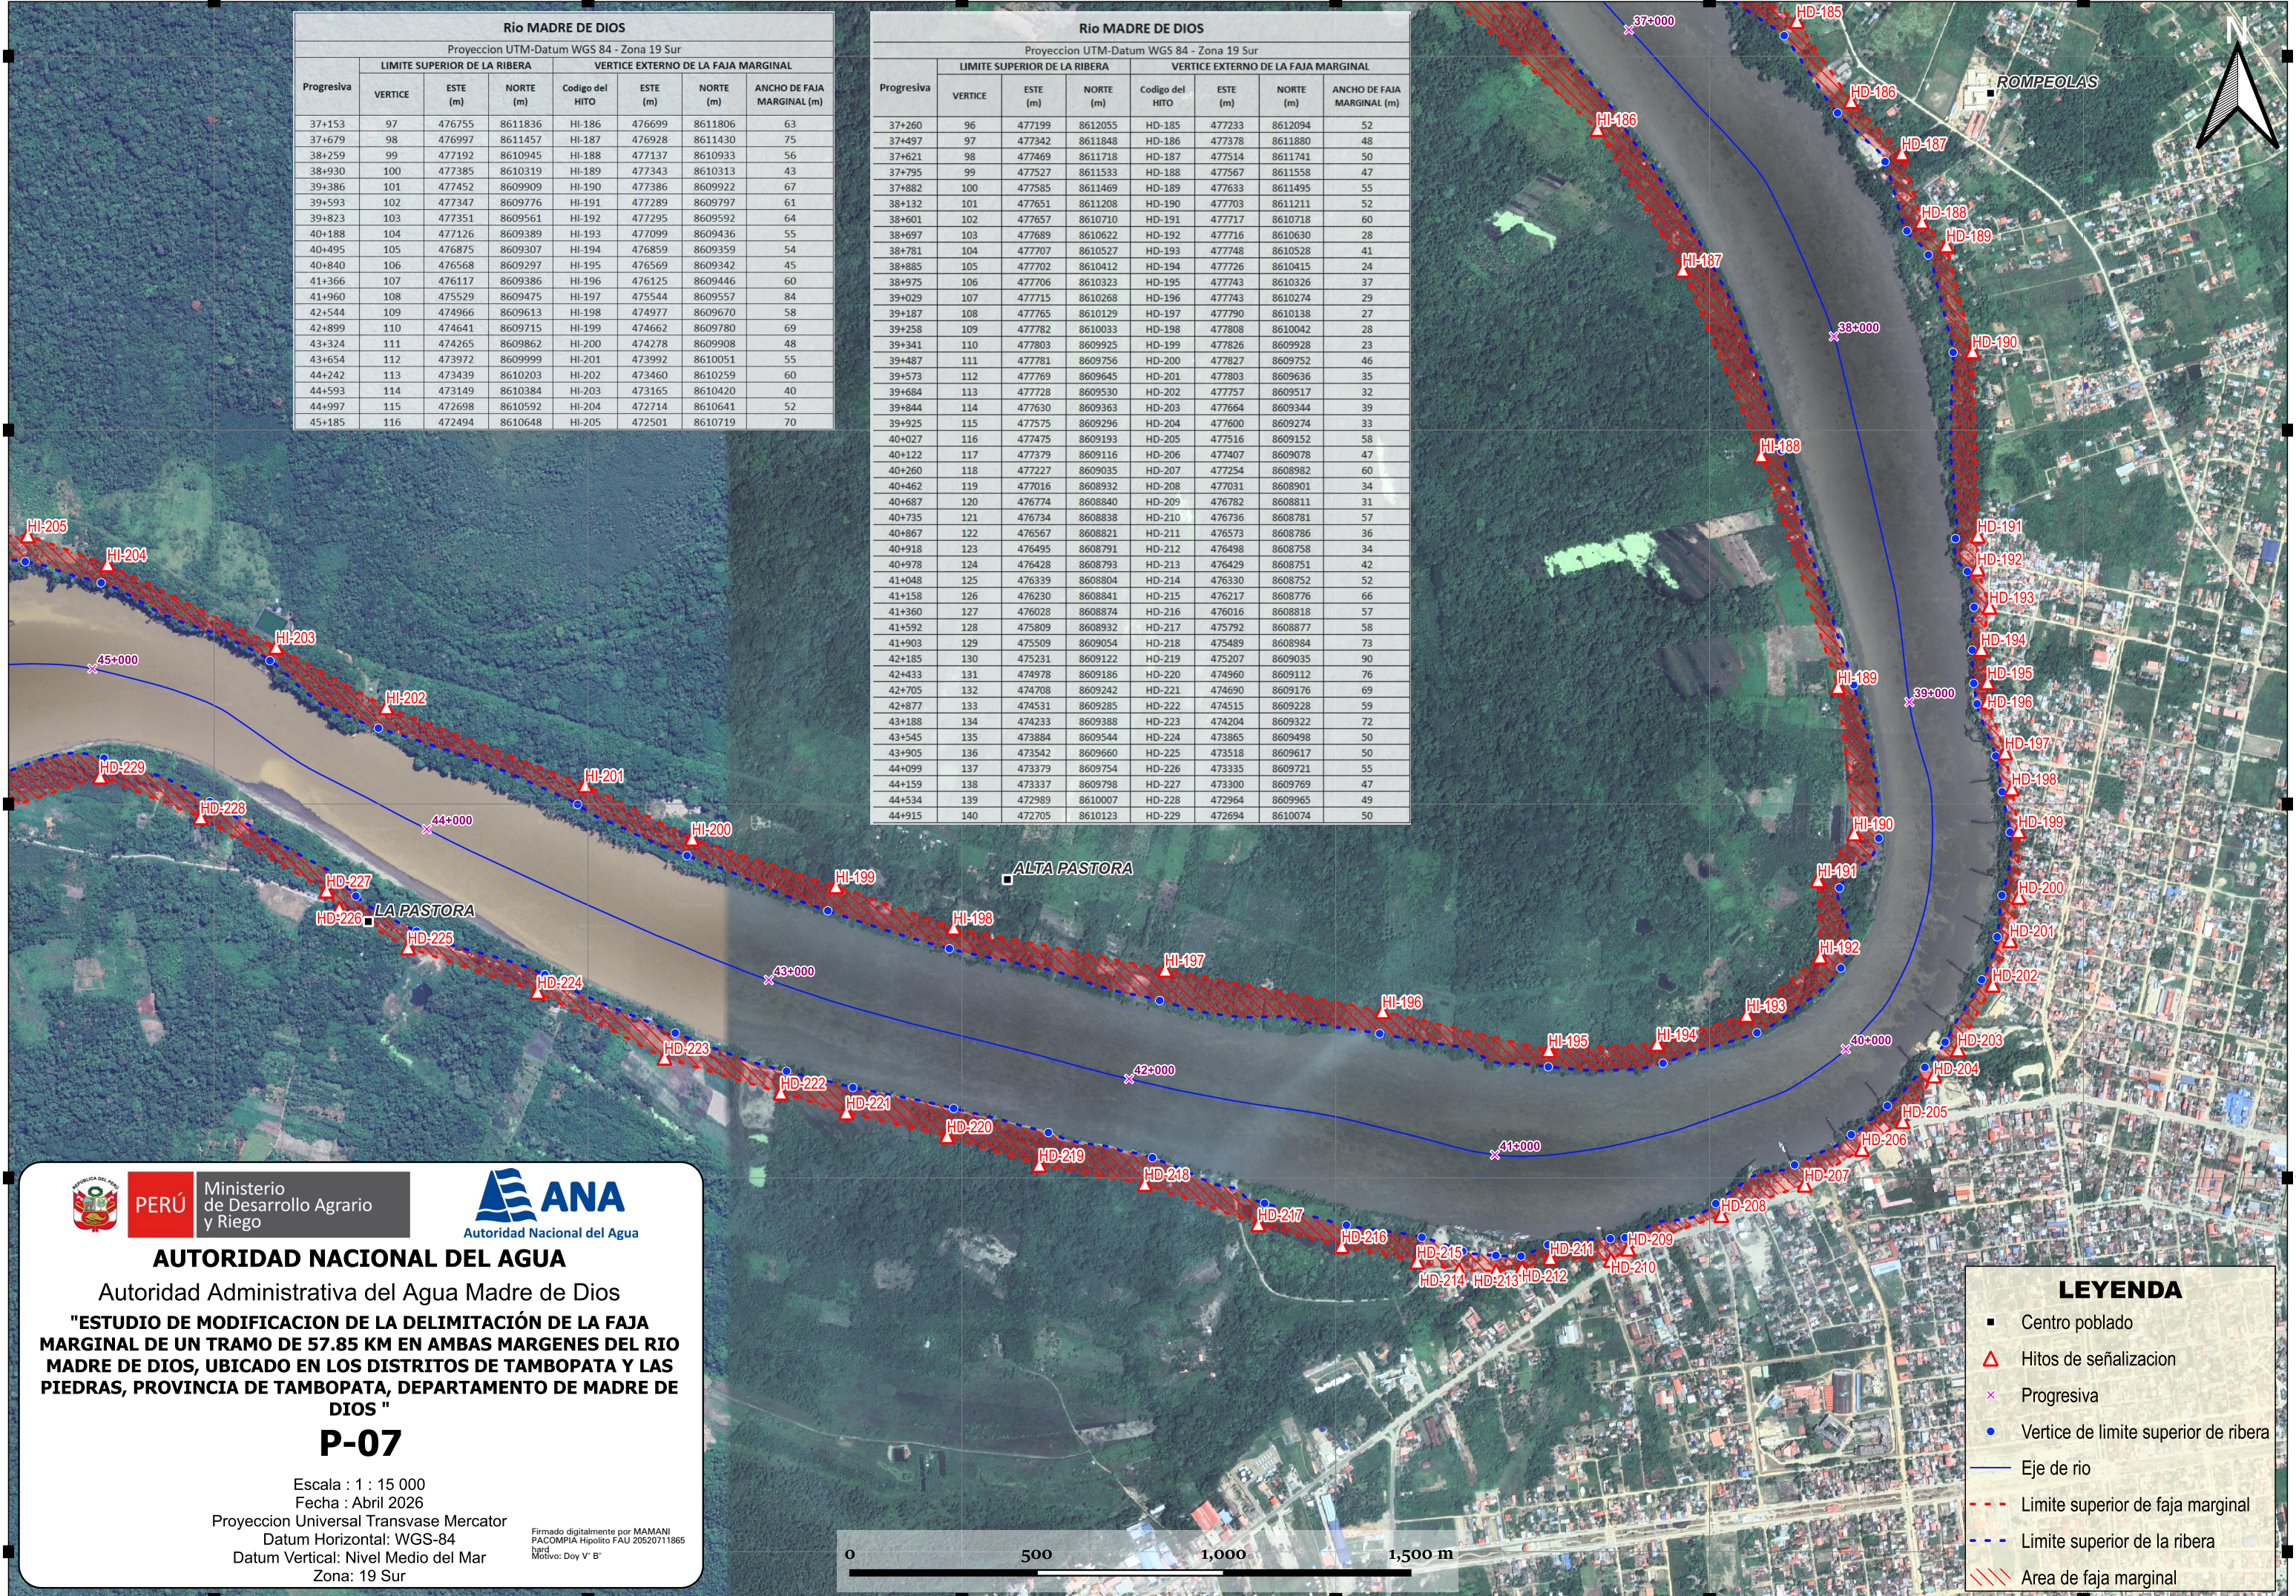

PERÚ

Ministerio
de Desarrollo Agrario
y Riego



ANA
Autoridad Nacional del Agua

AUTORIDAD NACIONAL DEL AGUA

Autoridad Administrativa del Agua Madre de Dios

"ESTUDIO DE MODIFICACION DE LA DELIMITACIÓN DE LA FAJA
MARGINAL DE UN TRAMO DE 57.85 KM EN AMBAS MARGENES DEL RIO
MADRE DE DIOS, UBICADO EN LOS DISTRITOS DE TAMBOPATA Y LAS
PIEDRAS, PROVINCIA DE TAMBOPATA, DEPARTAMENTO DE MADRE DE
DIOS "

P-07

Escala : 1 : 15 000

Fecha : Abril 2026

Proyeccion Universal Transvase Mercator

Datum Horizontal: WGS-84

Datum Vertical: Nivel Medio del Mar

Zona: 19 Sur

Firmado digitalmente por MAMANI
PACOMPIA Hipolito FAU 20520711865
Motivo: Doy V° B°

LEYENDA

- Centro poblado
- Hitos de señalizacion
- Progresiva
- Vertice de limite superior de ribera
- Eje de rio
- Limite superior de faja marginal
- Limite superior de la ribera
- Area de faja marginal