

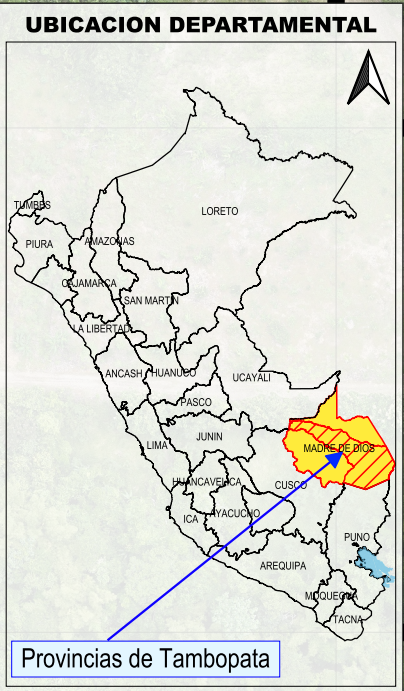


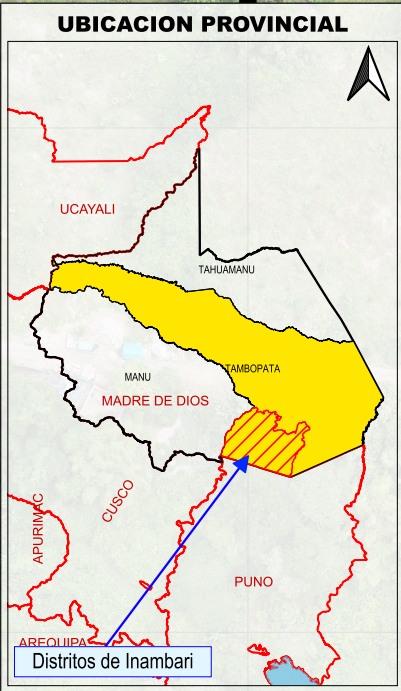

- LEYENDA**
- △ Hito de señalizacion
 - Entre vertice
 - × Progresiva
 - Vertice de limite superior de la ribera
 - Eje de quebrada
 - - - Limite superior de faja marginal
 - - - Limite superior de la ribera
 - ▨ Gabiones
 - ▨ Area de faja marginal

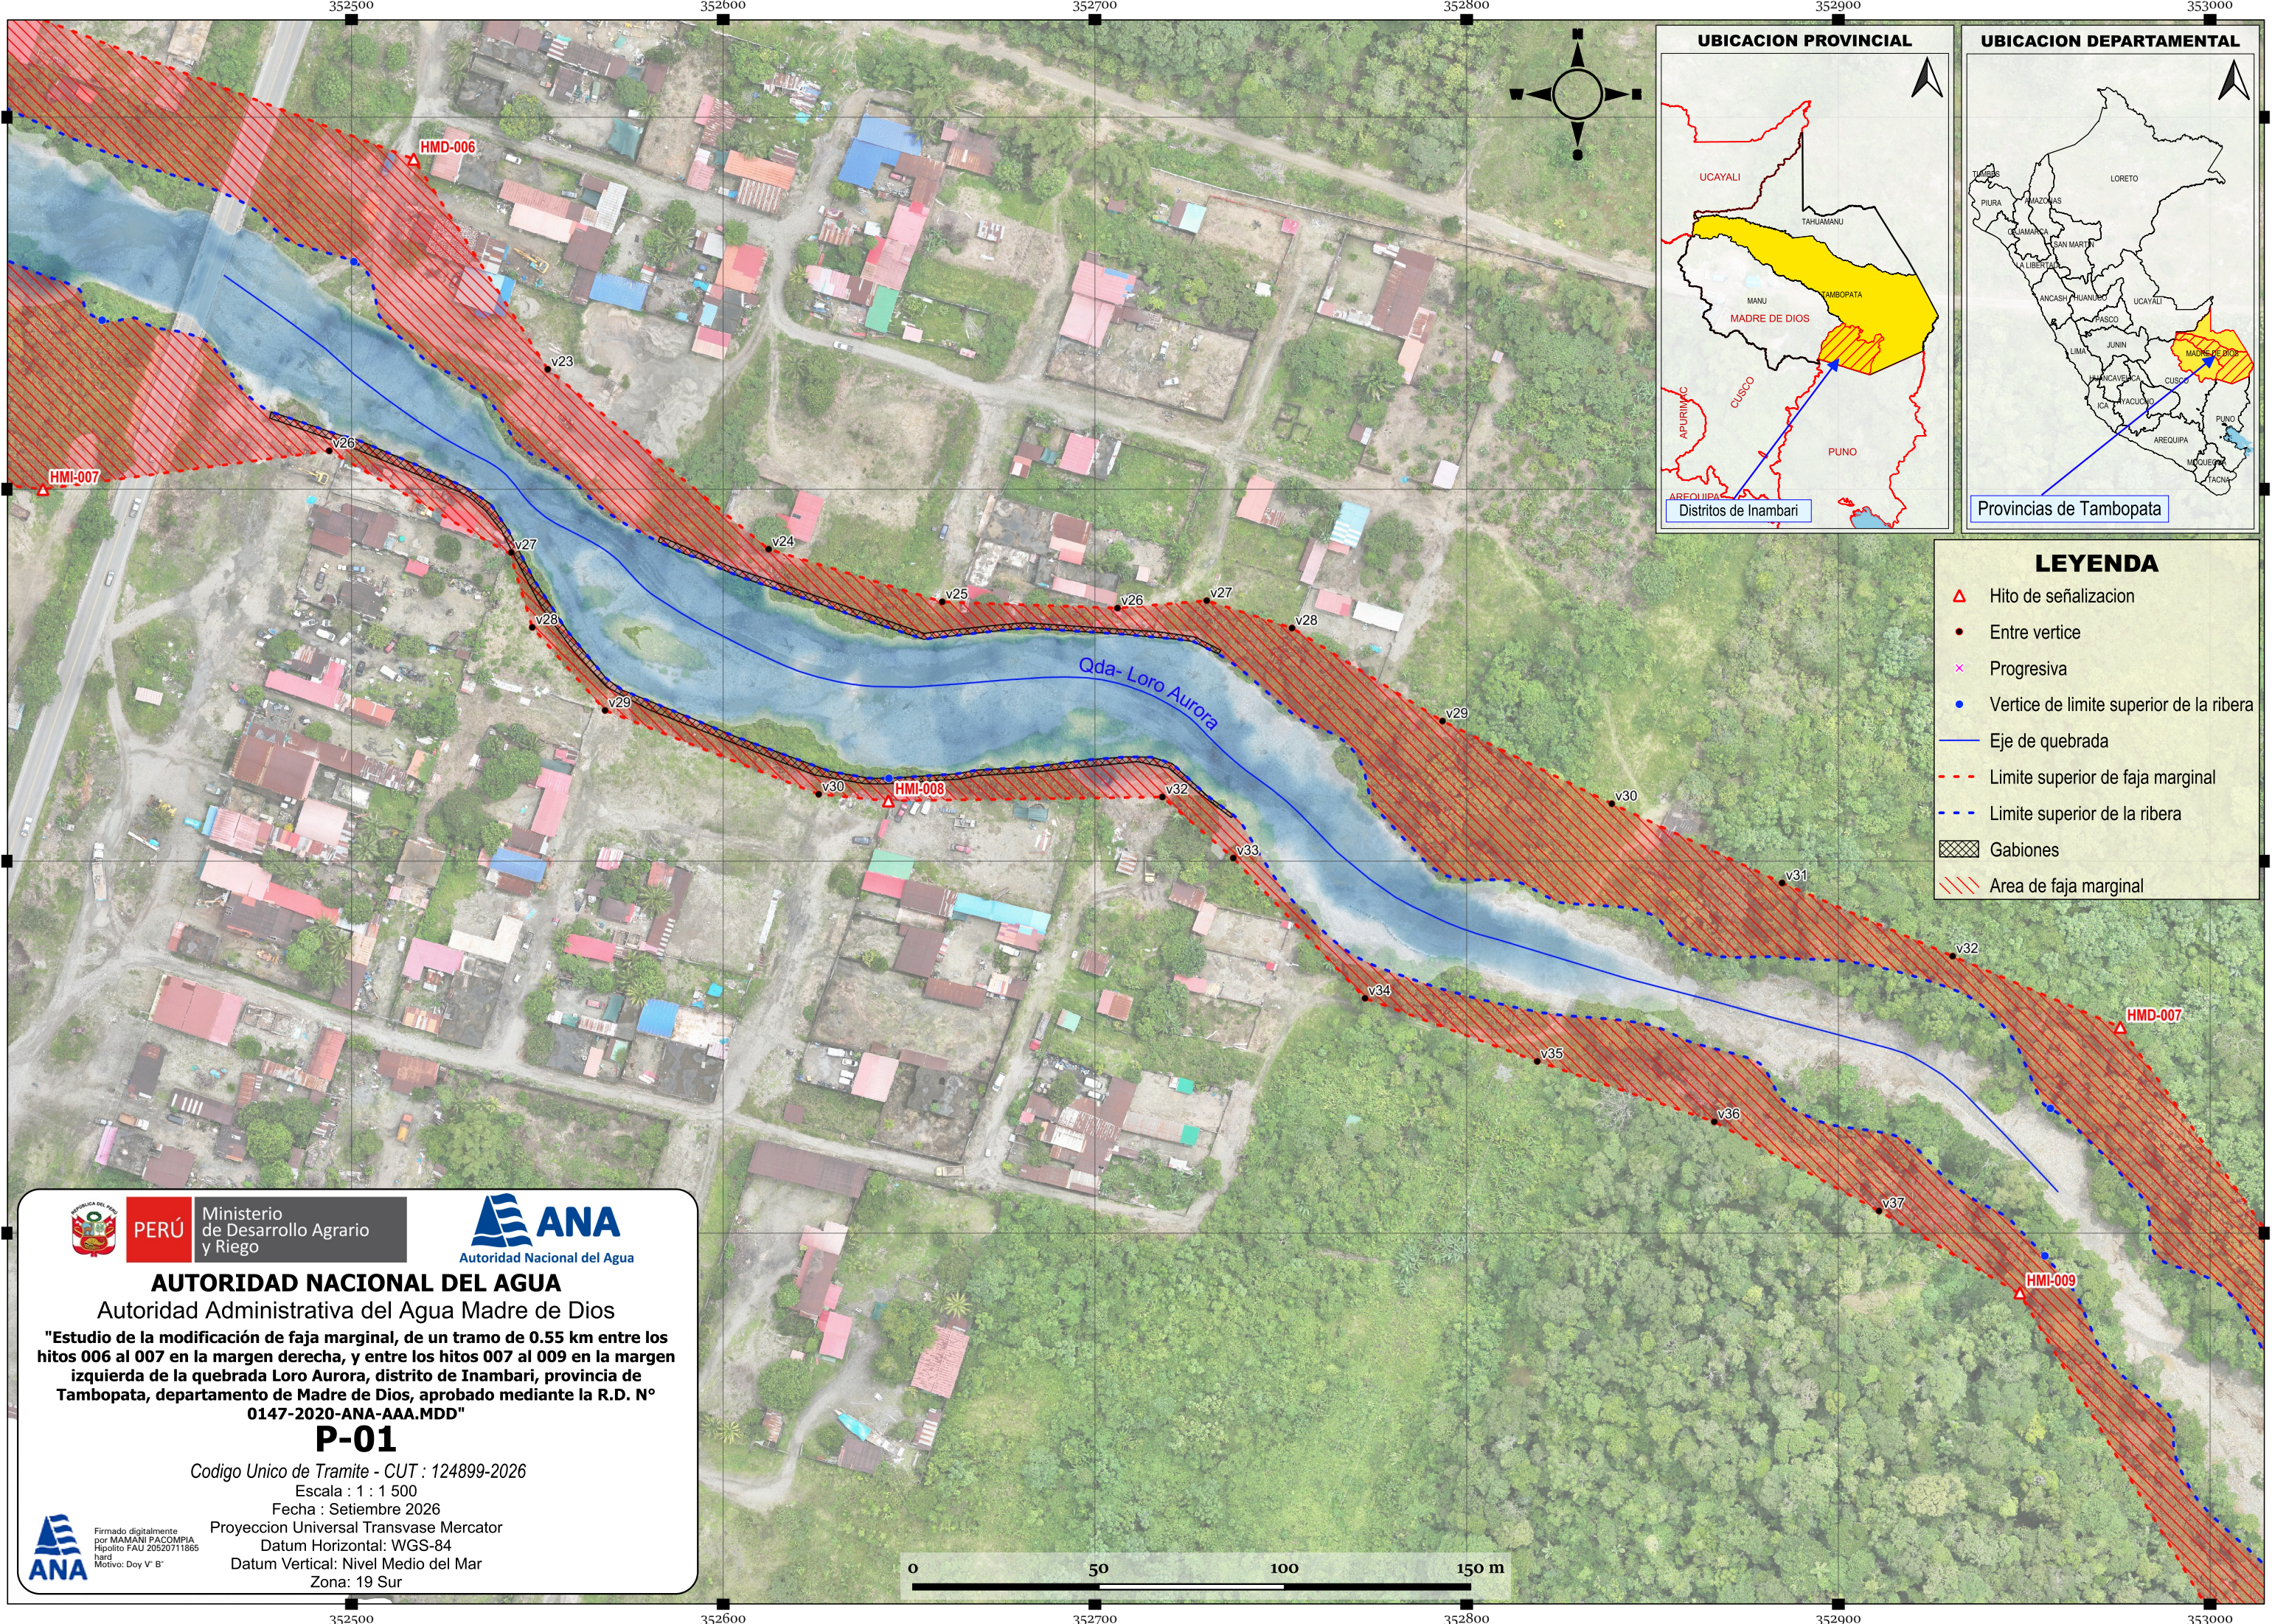

PERÚ

Ministerio
de Desarrollo Agrario
y Riego



ANA
Autoridad Nacional del Agua

AUTORIDAD NACIONAL DEL AGUA

Autoridad Administrativa del Agua Madre de Dios

"Estudio de la modificación de faja marginal, de un tramo de 0.55 km entre los hitos 006 al 007 en la margen derecha, y entre los hitos 007 al 009 en la margen izquierda de la quebrada Loro Aurora, distrito de Inambari, provincia de Tambopata, departamento de Madre de Dios, aprobado mediante la R.D. N° 0147-2020-ANA-AAA.MDD"

P-01

Codigo Unico de Tramite - CUT : 124899-2026

Escala : 1 : 1 500

Fecha : Setiembre 2026

Proyeccion Universal Transvase Mercator

Datum Horizontal: WGS-84

Datum Vertical: Nivel Medio del Mar

Zona: 19 Sur



Firmado digitalmente
por MANANI PACOMPIA
Hipólito FAU 20520711865
hard
Motivo: Doy V° B°

0 50 100 150 m